




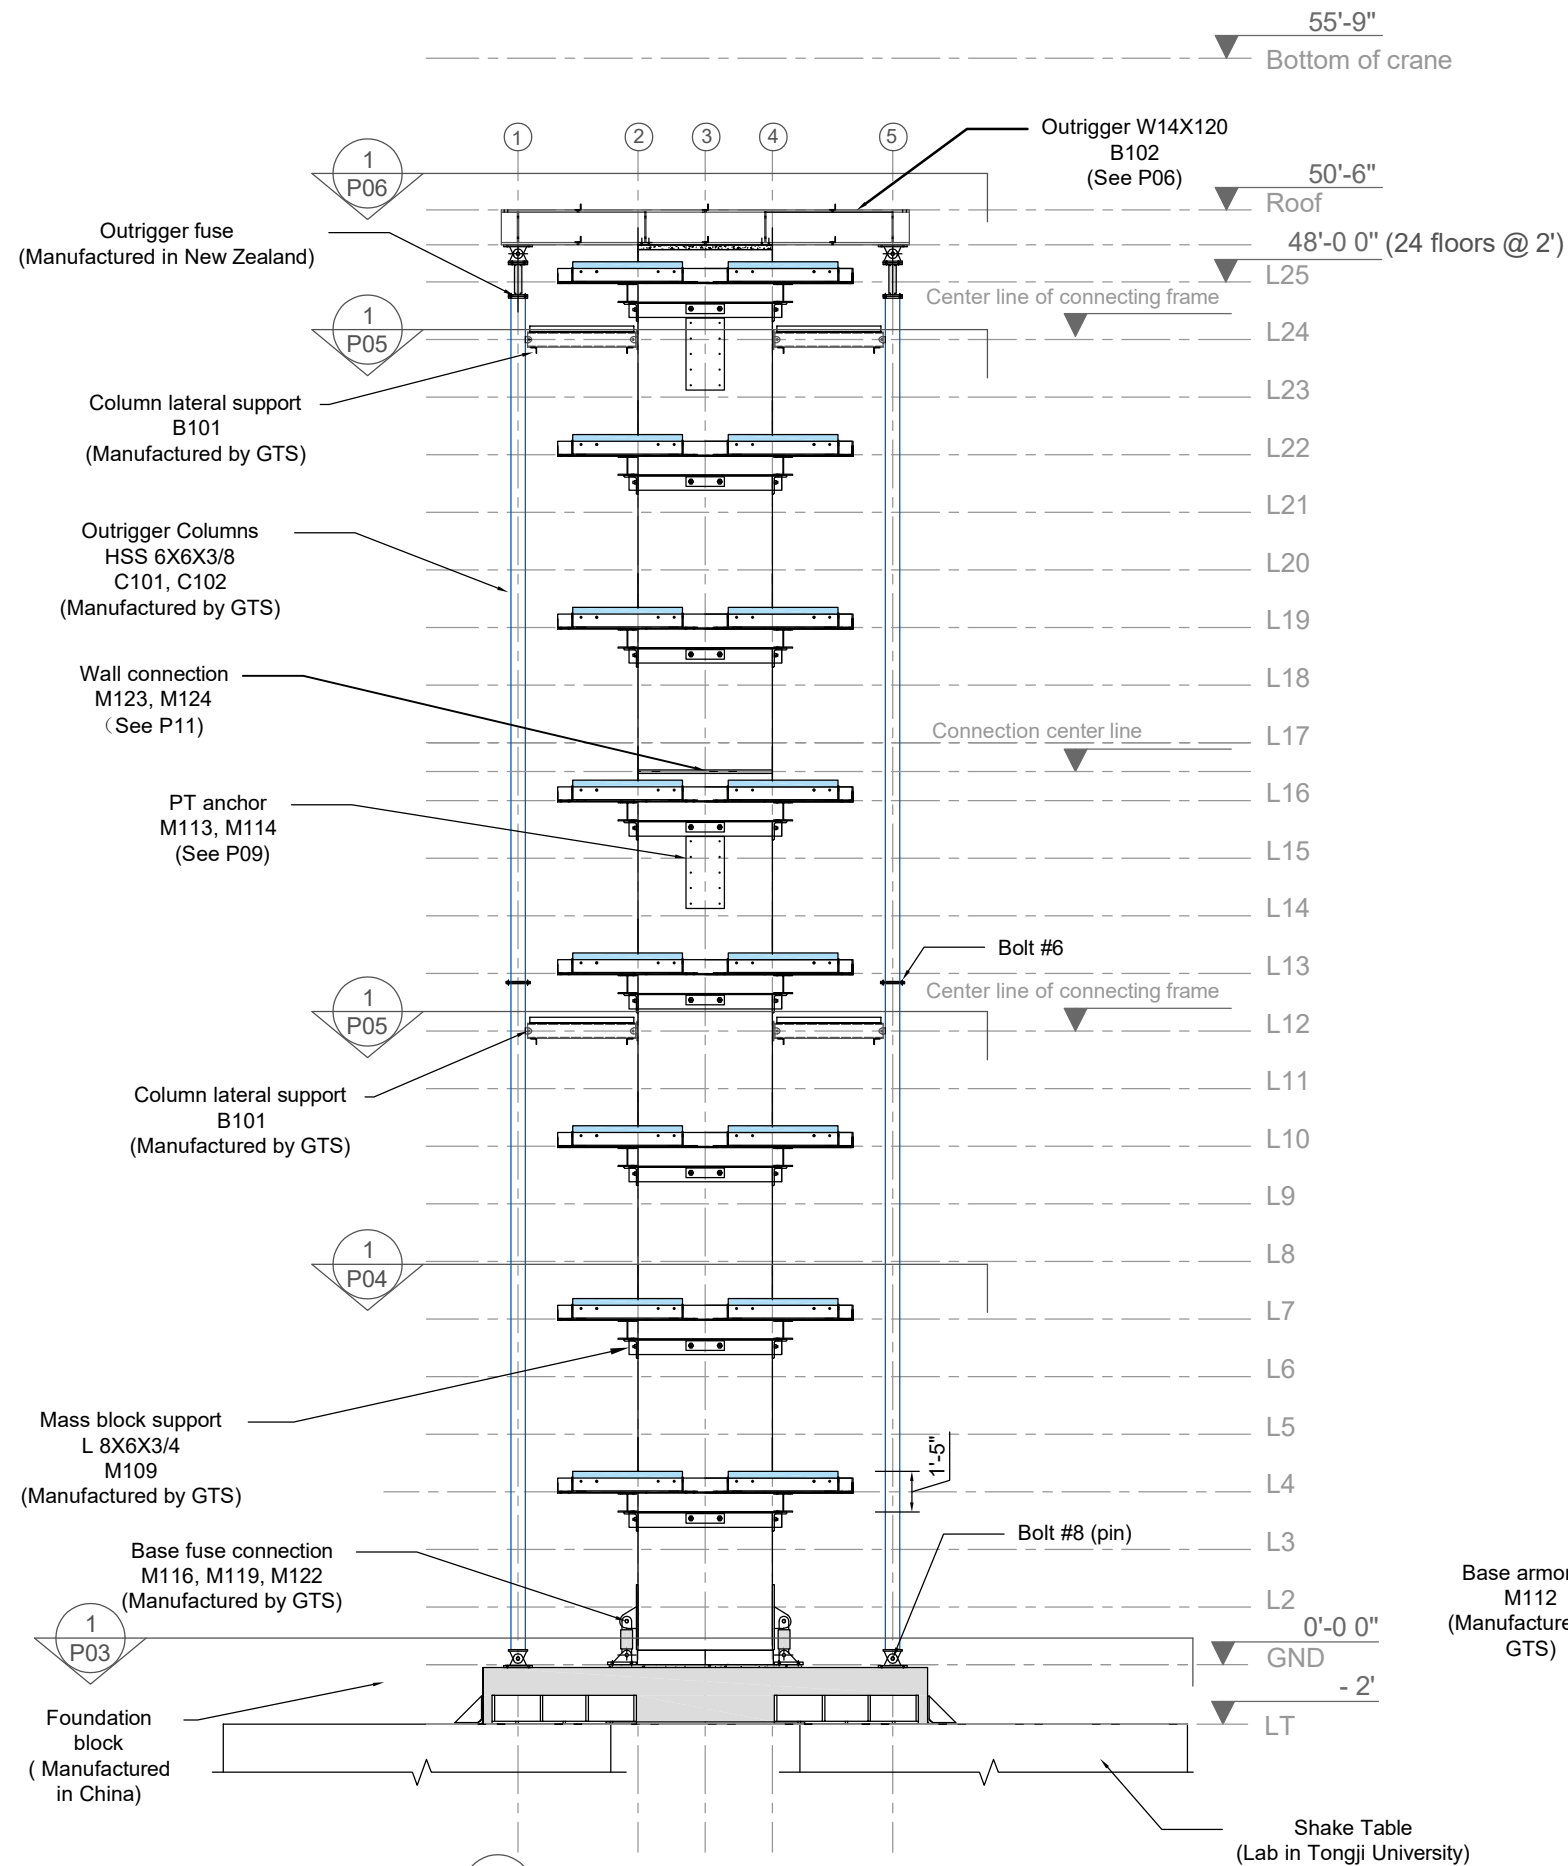


Test set-up: front view

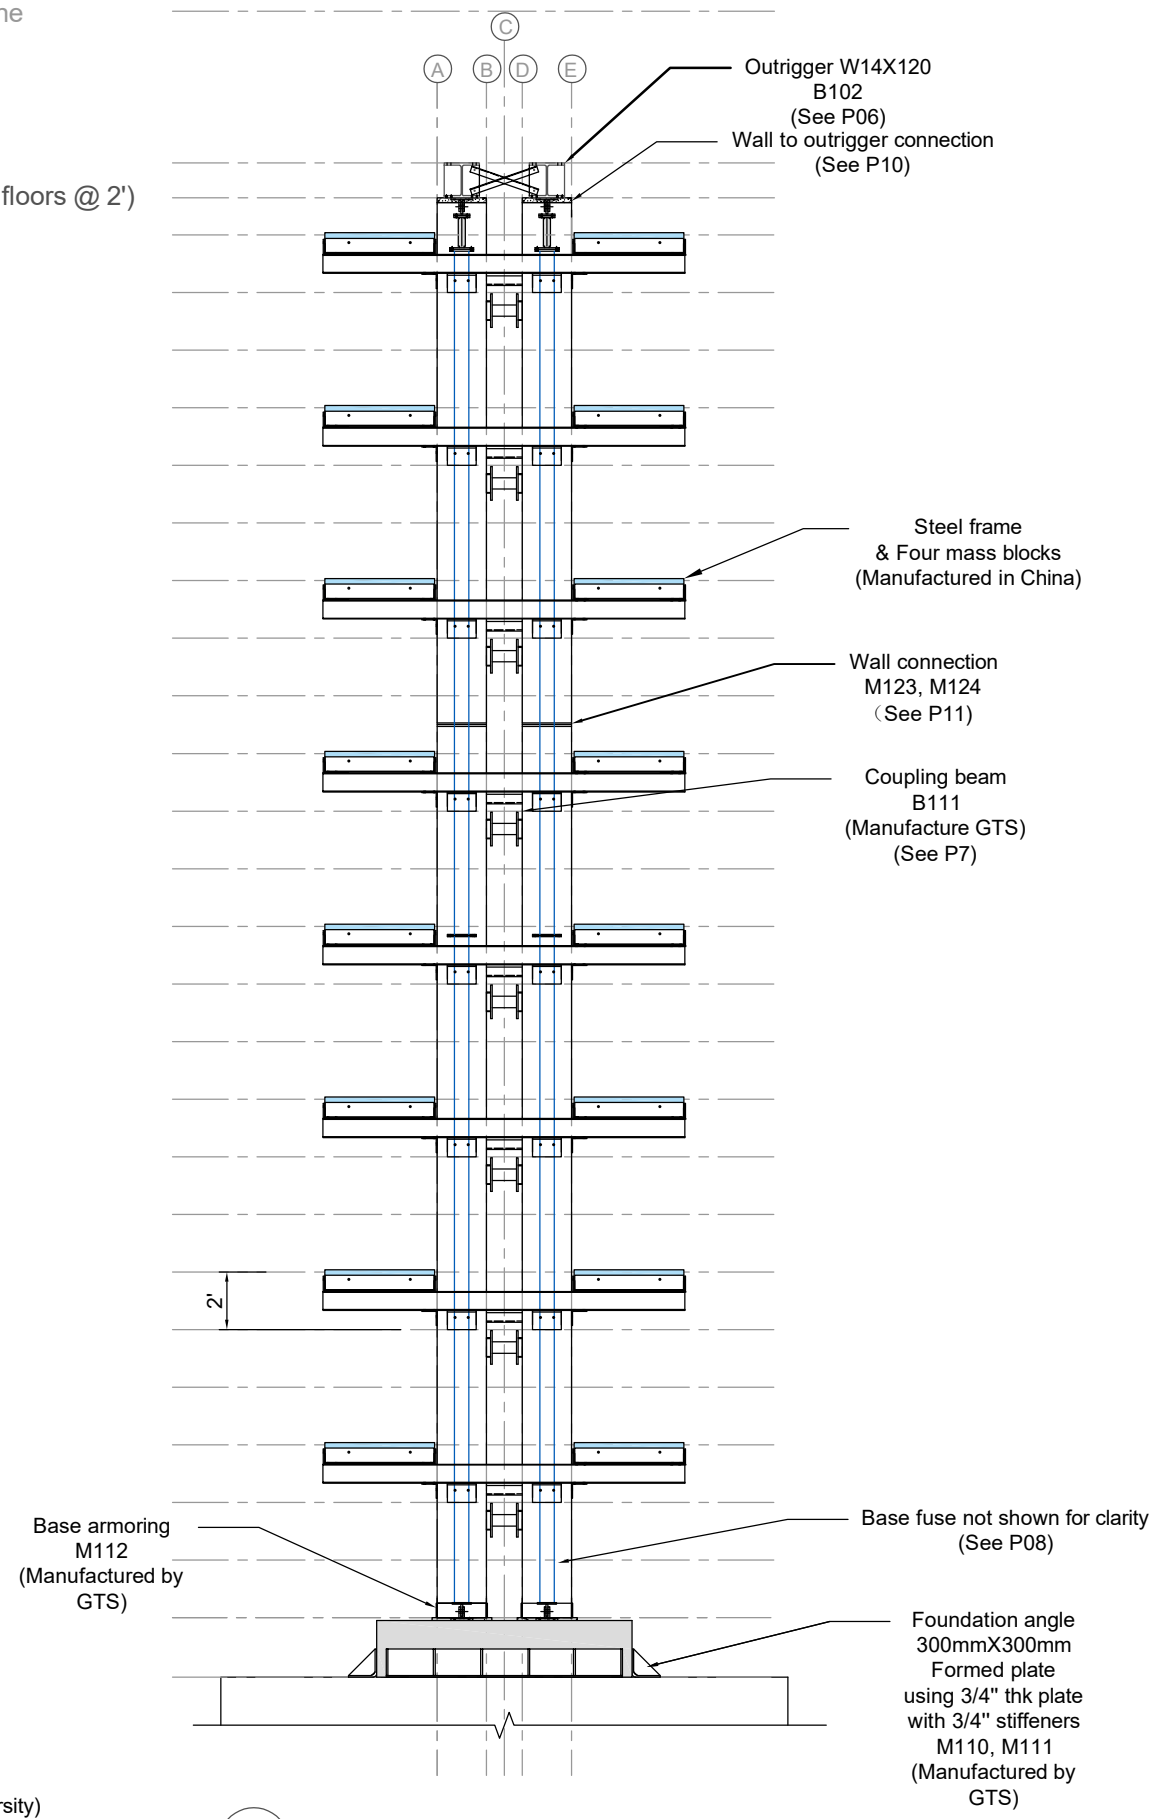


Test set-up: side view

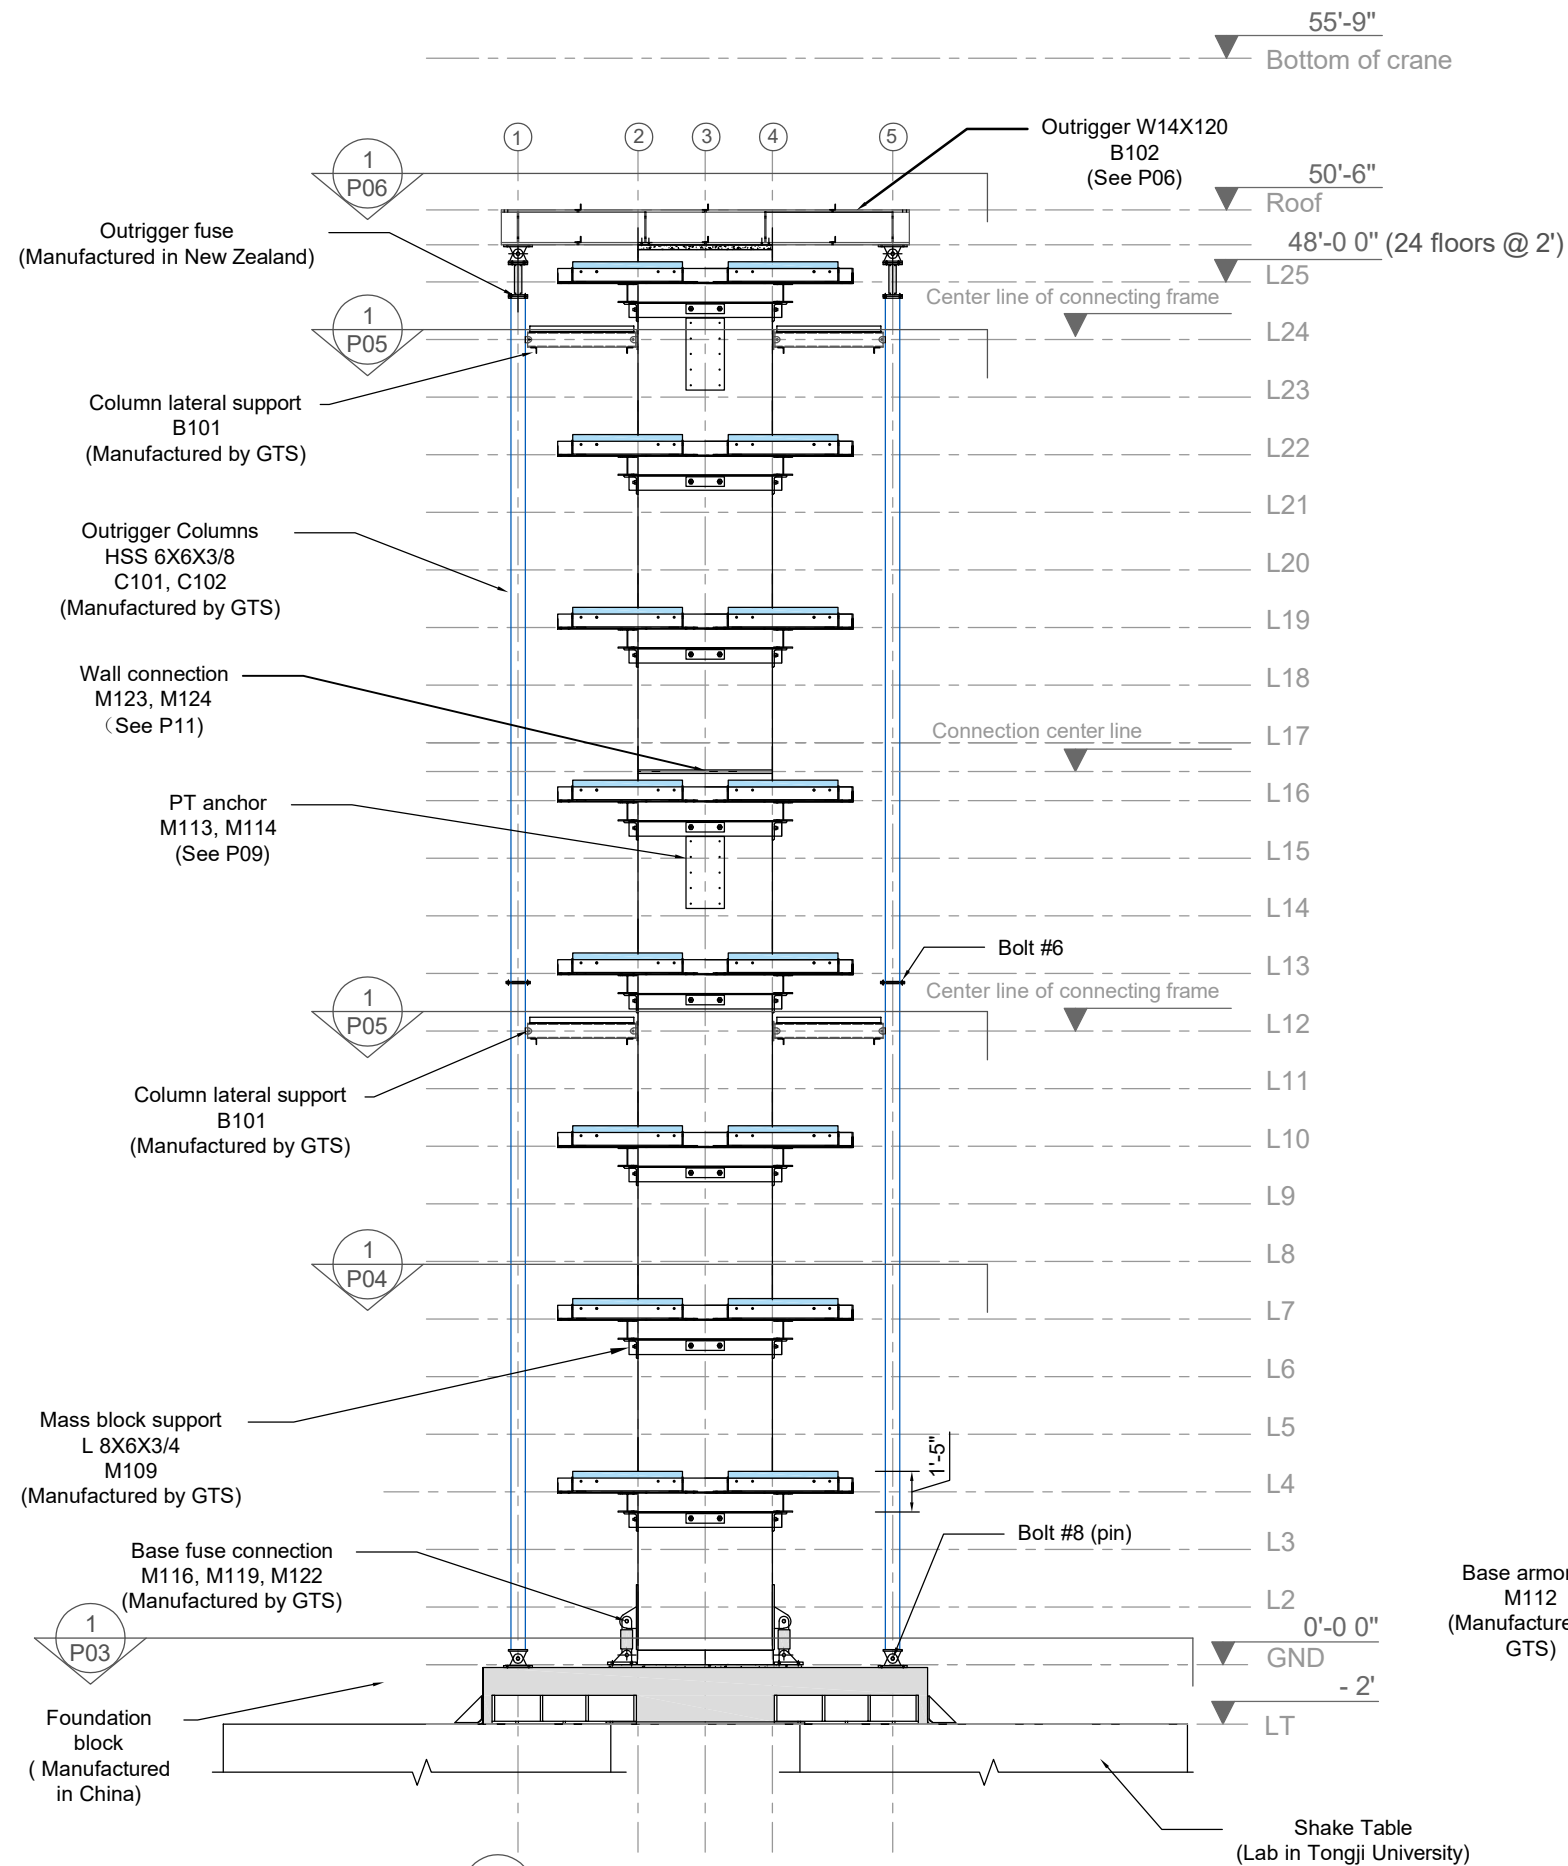


Test set-up: front view

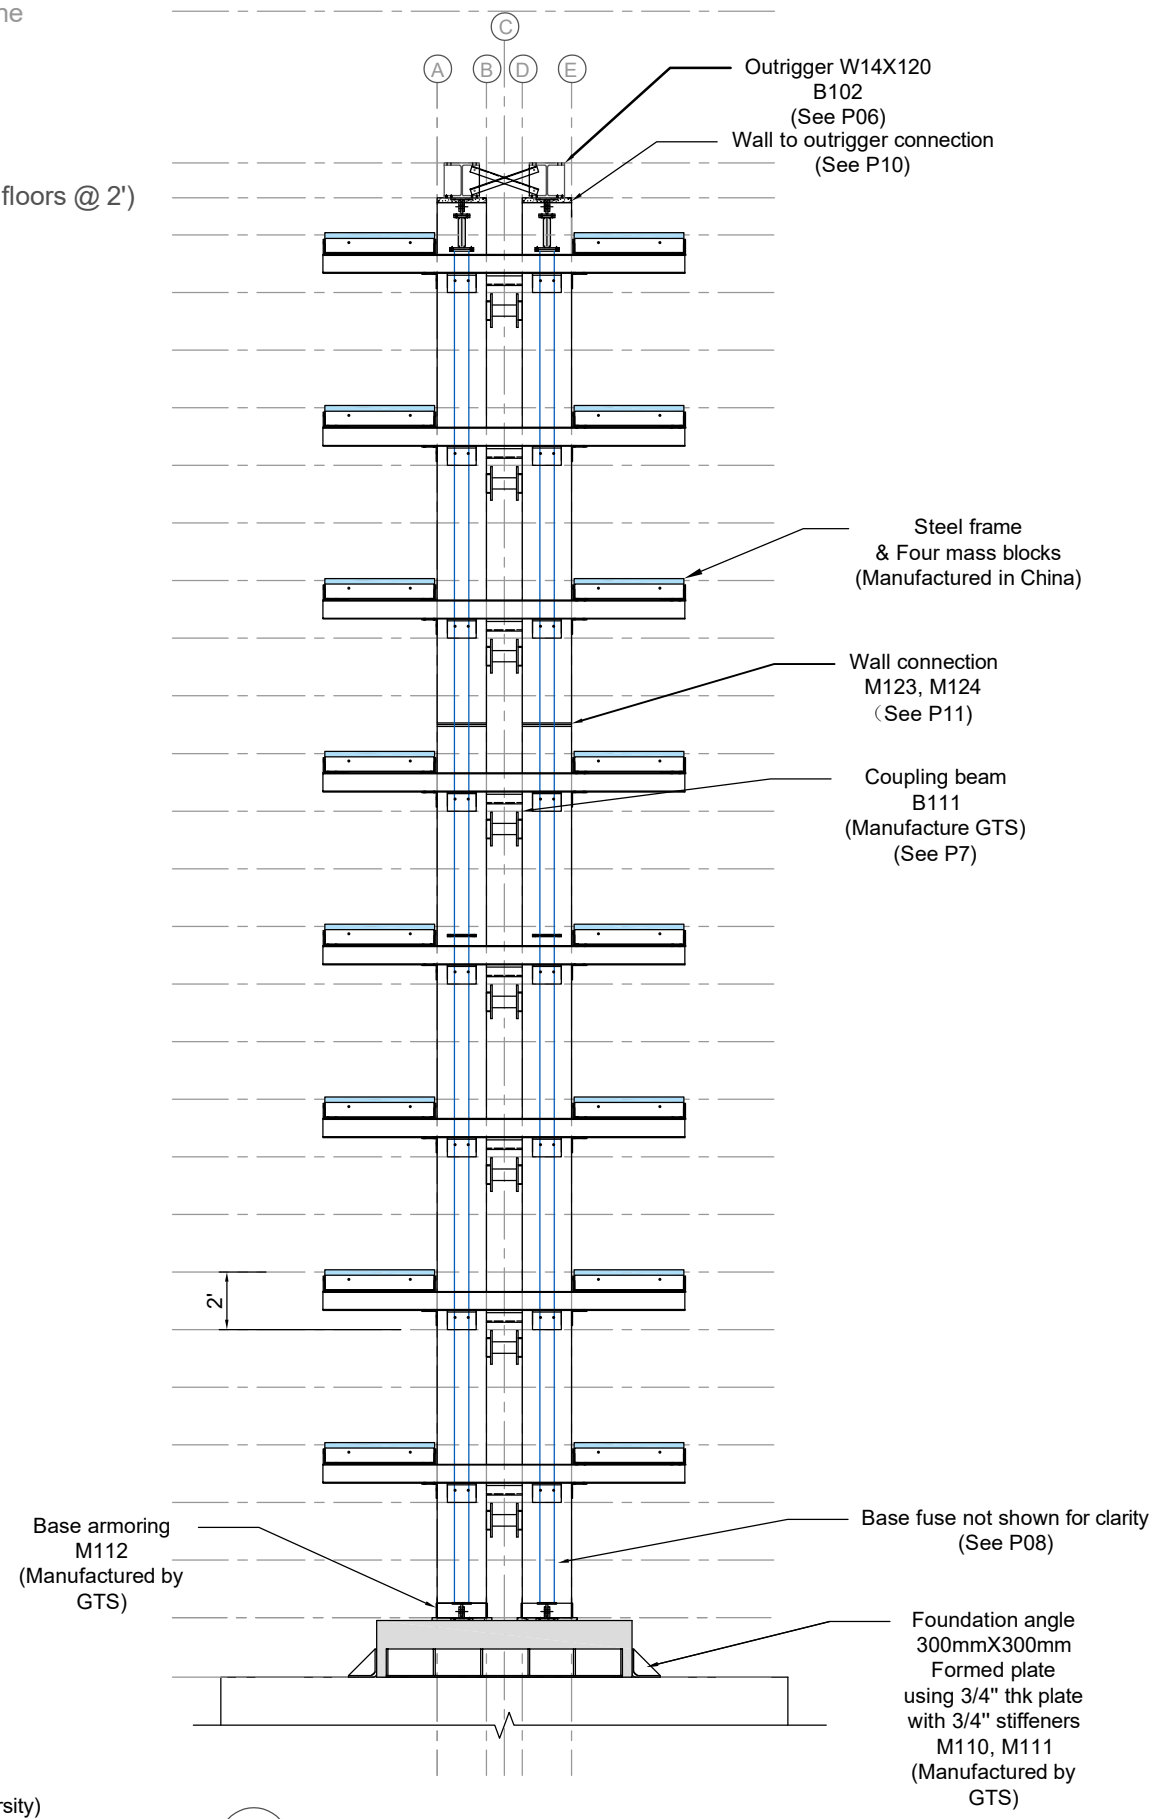


Test set-up: side view



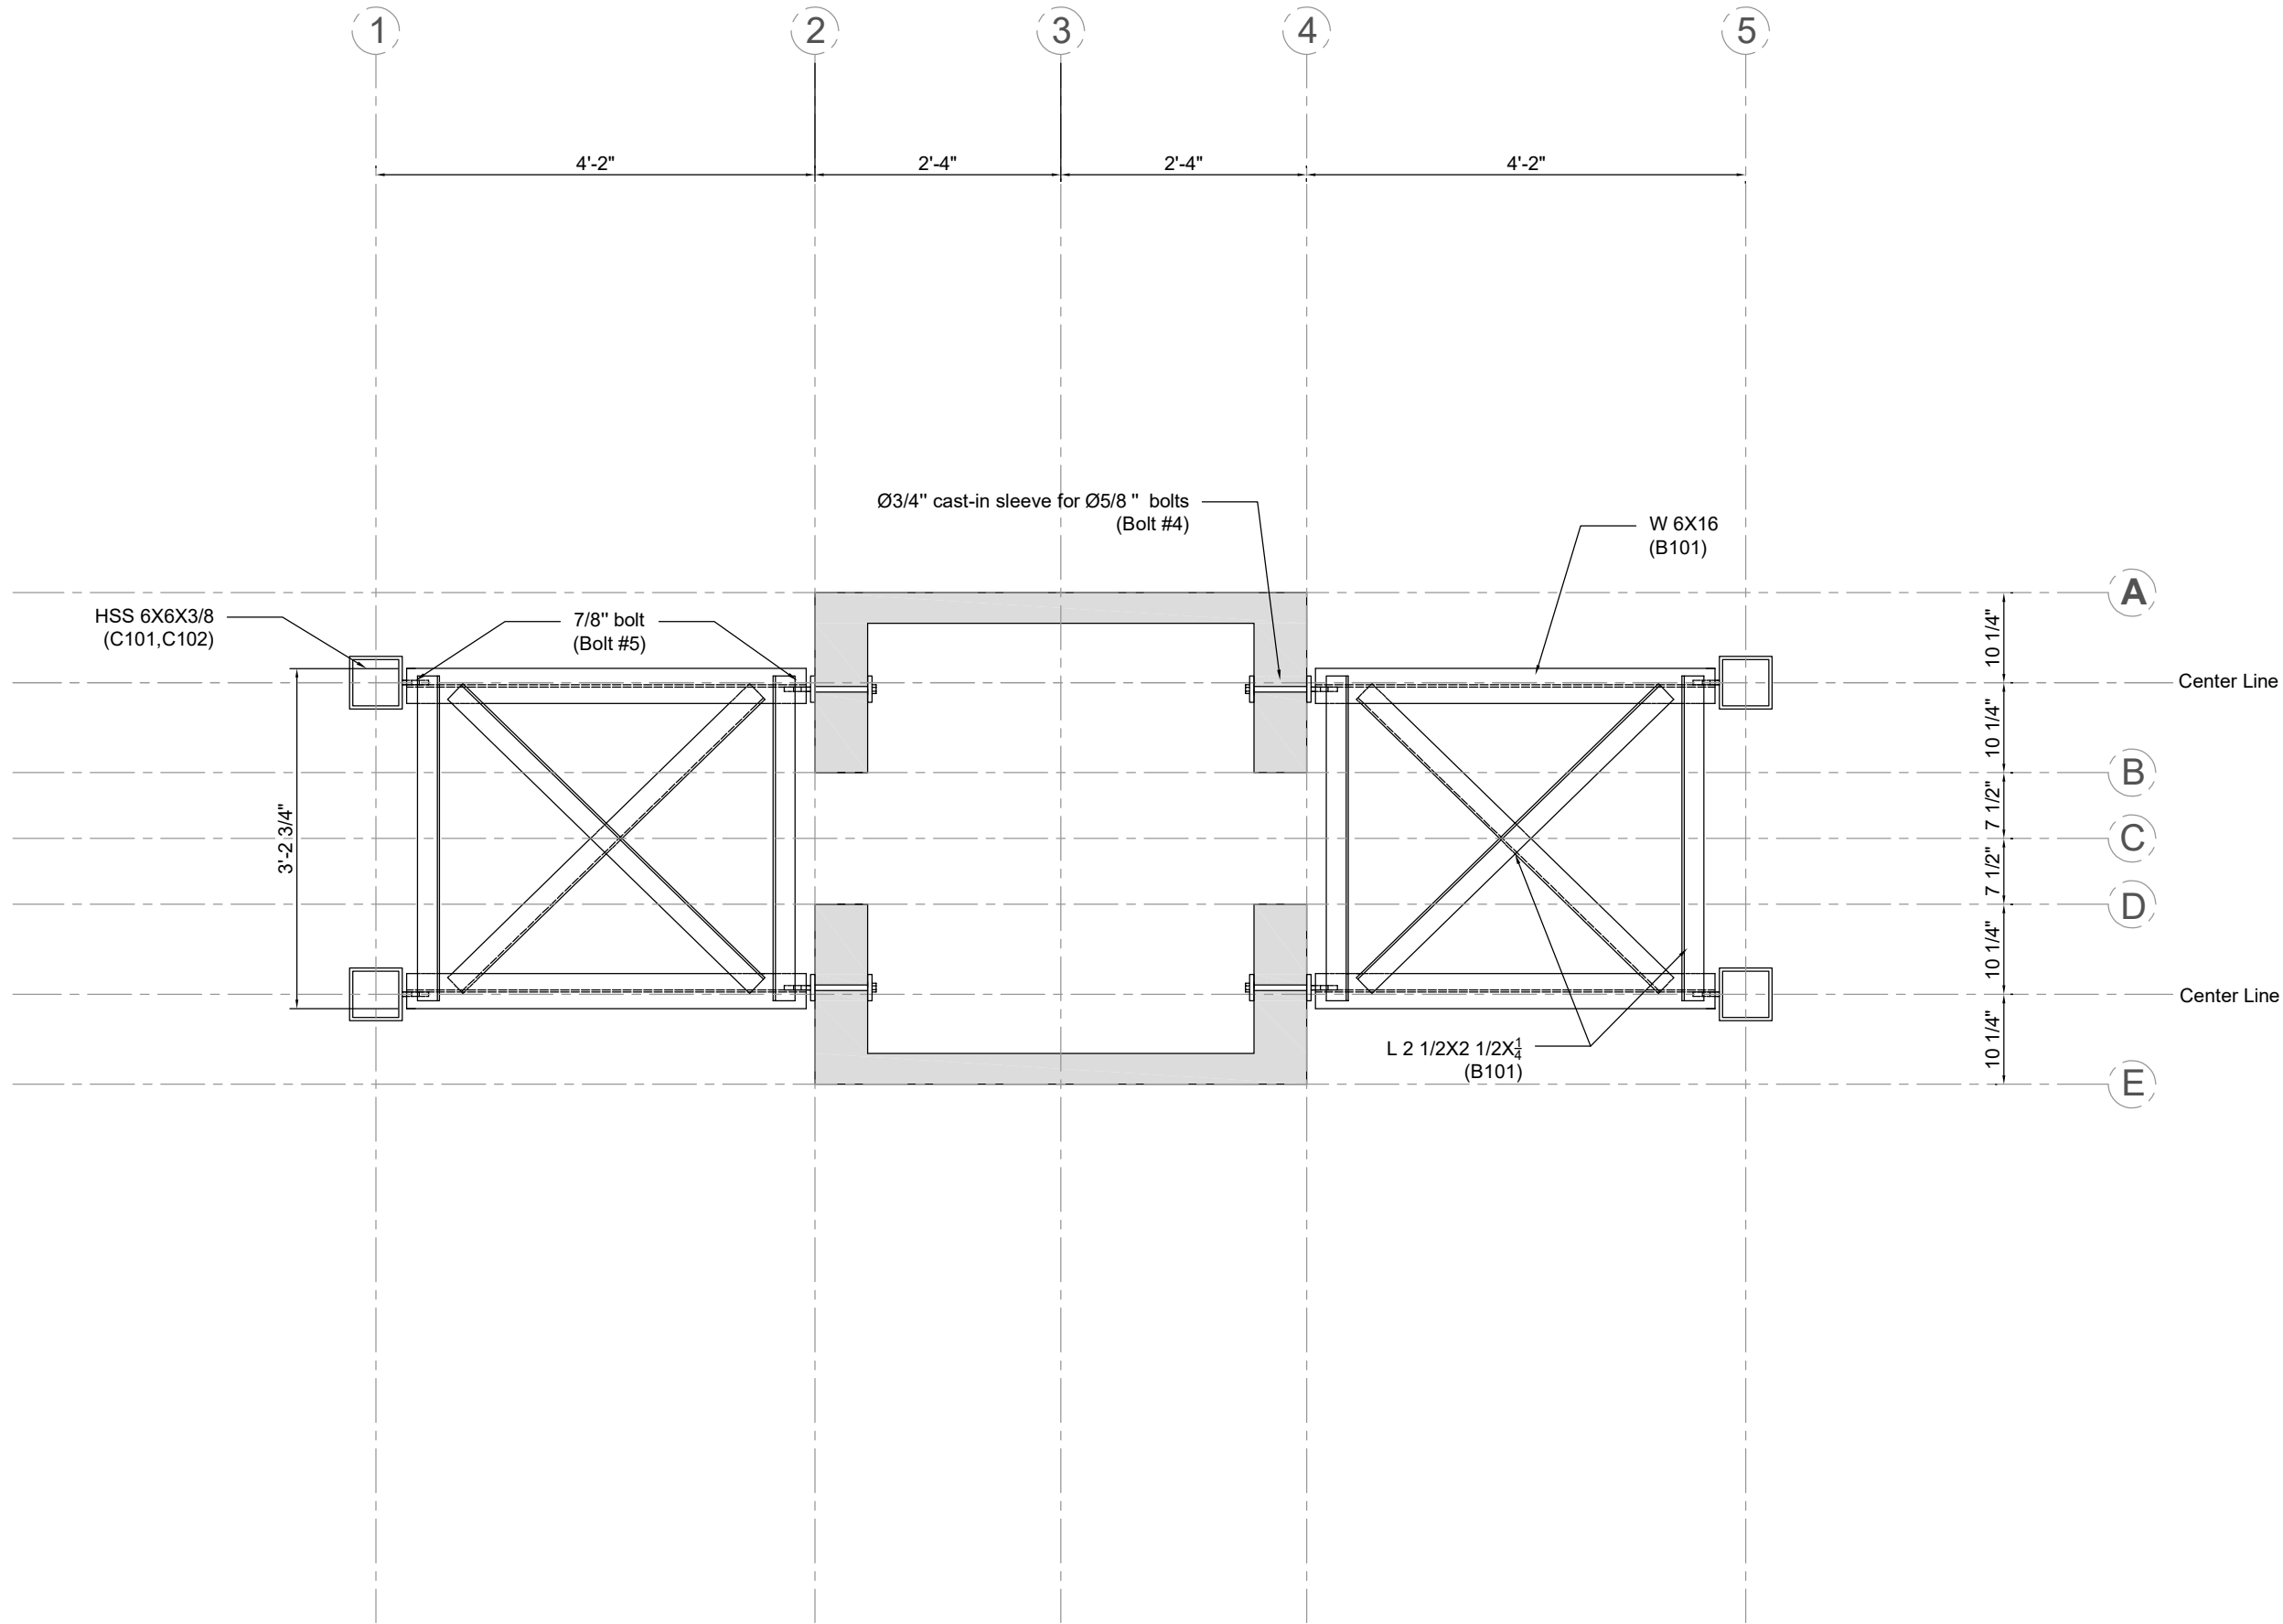


Note for elevation of lateral support:
240" (L11) & 552" (L24)

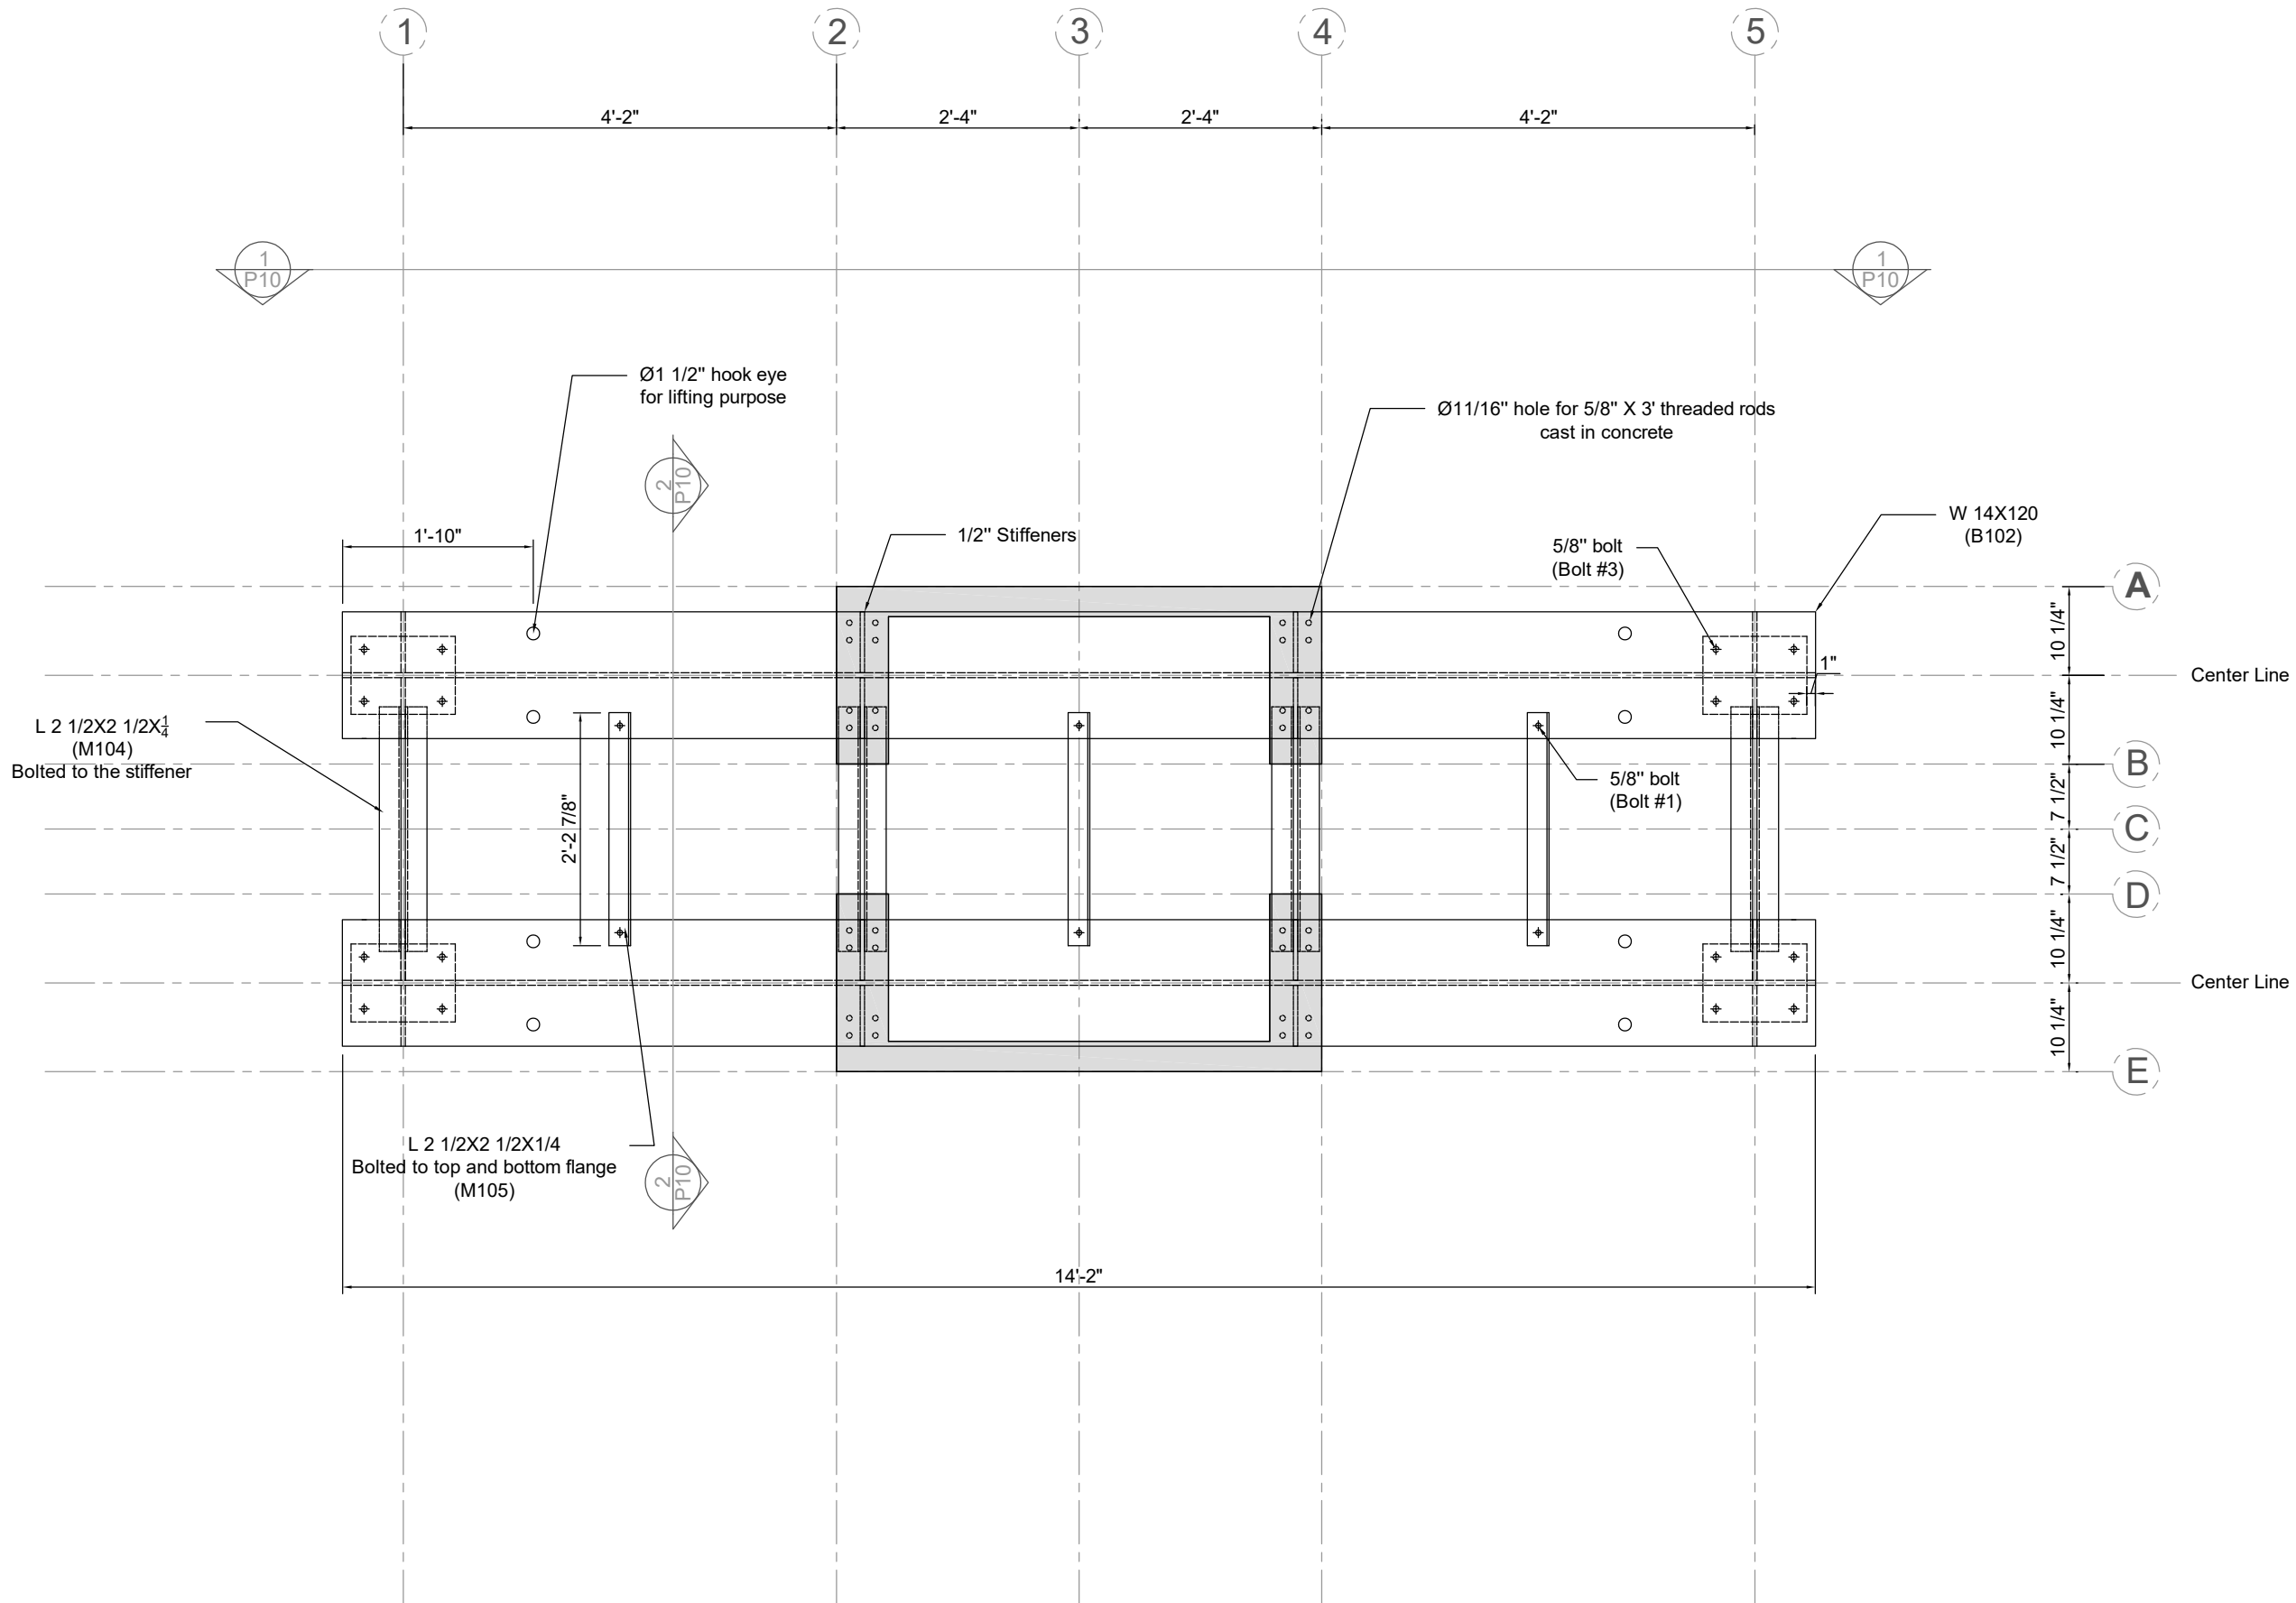



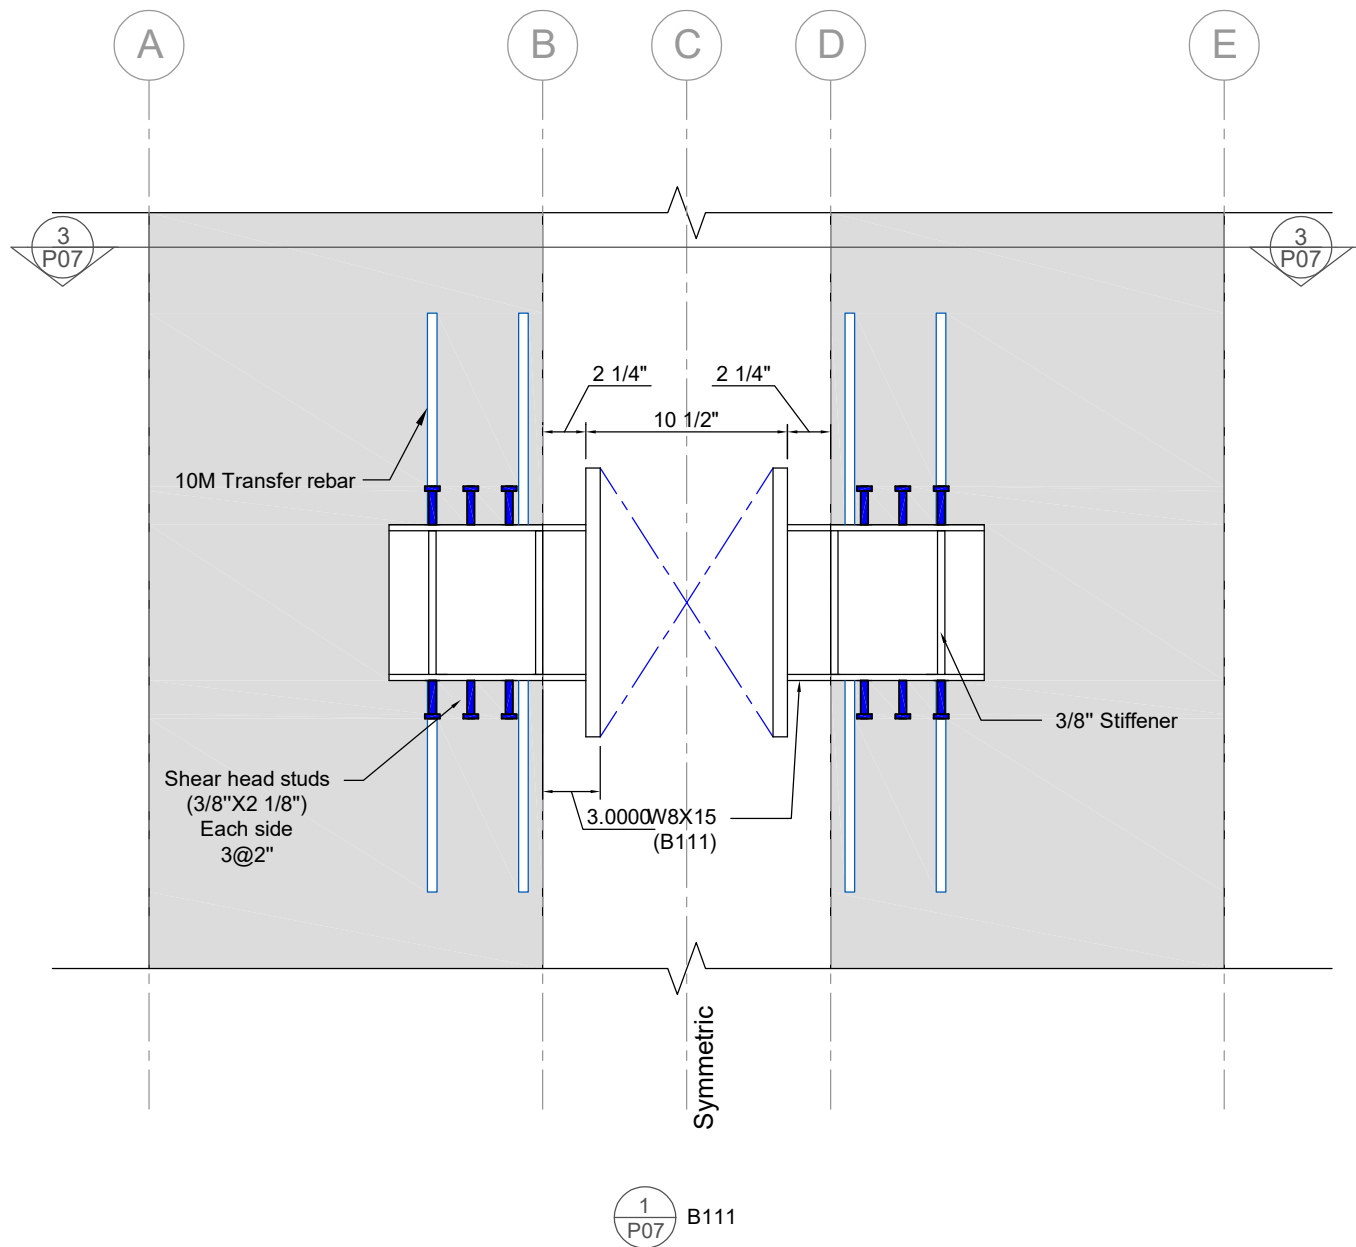



1 P07 B111

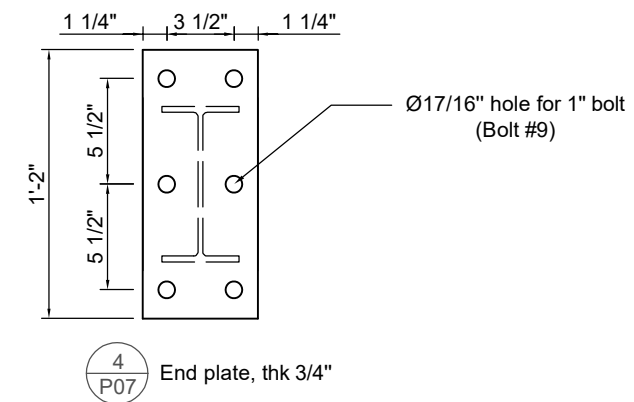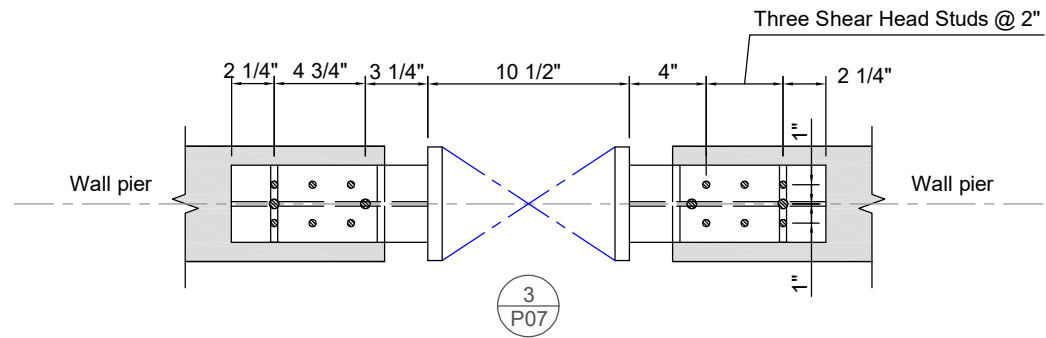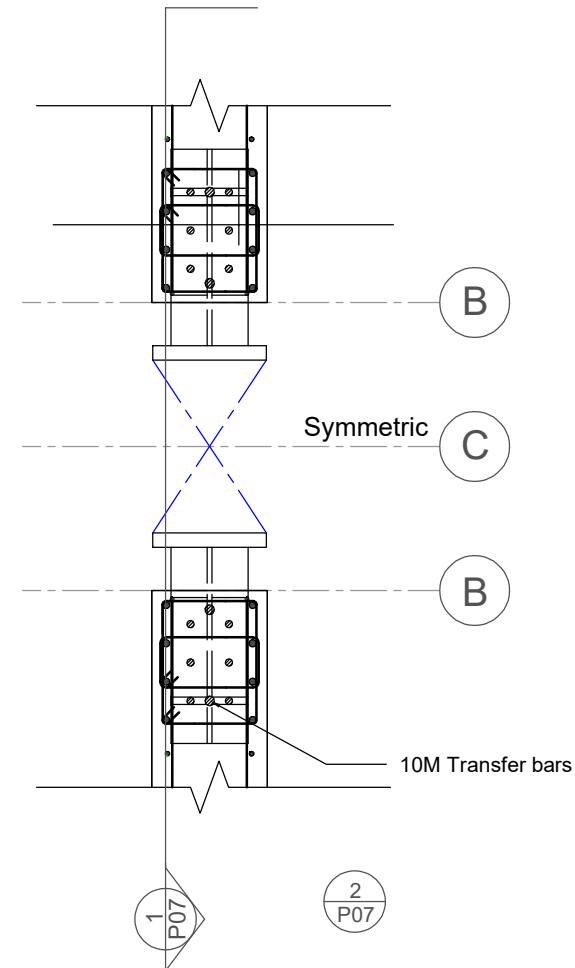


4 P07 End plate, thk 3/4"

L1

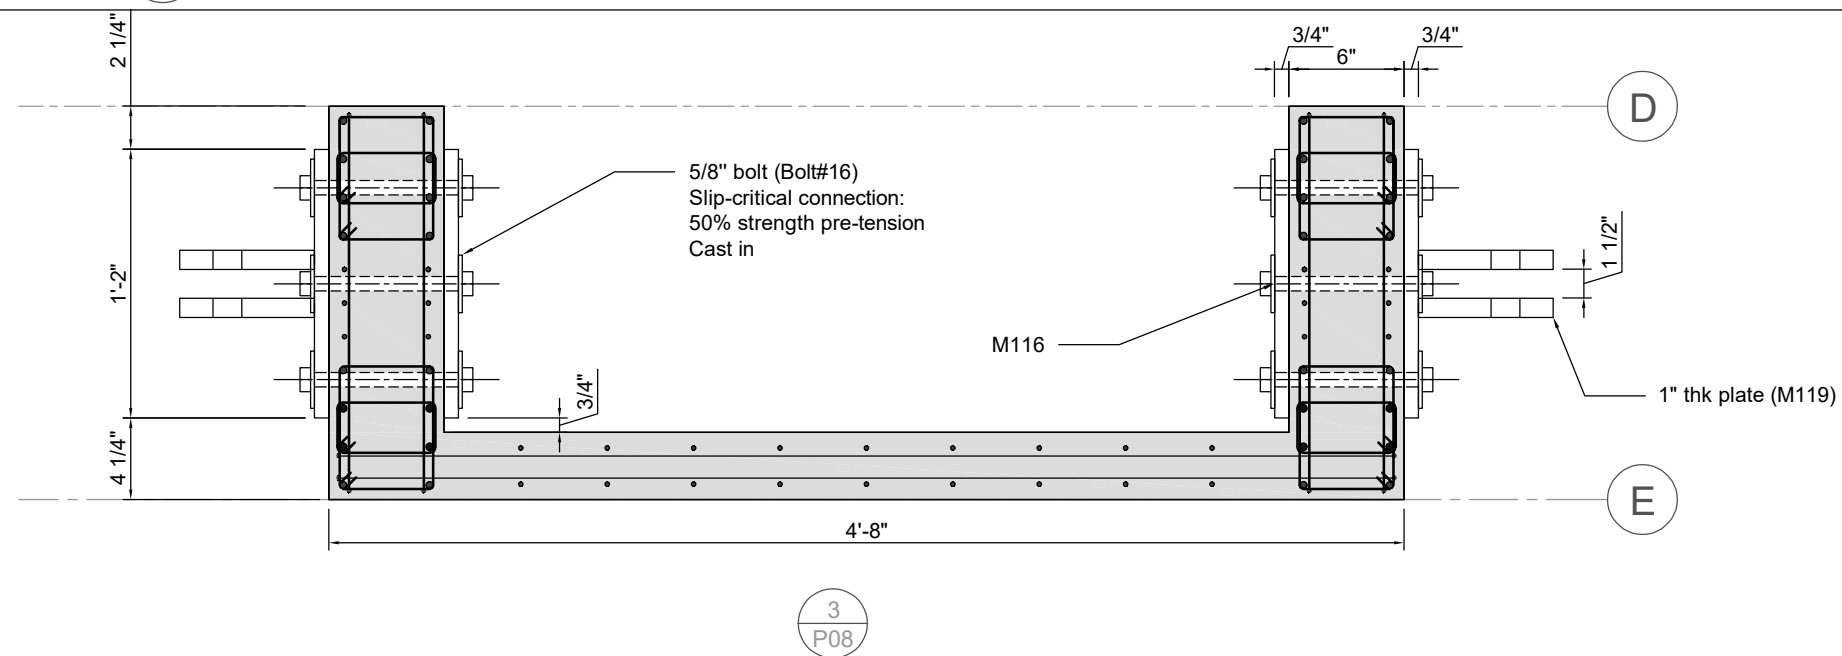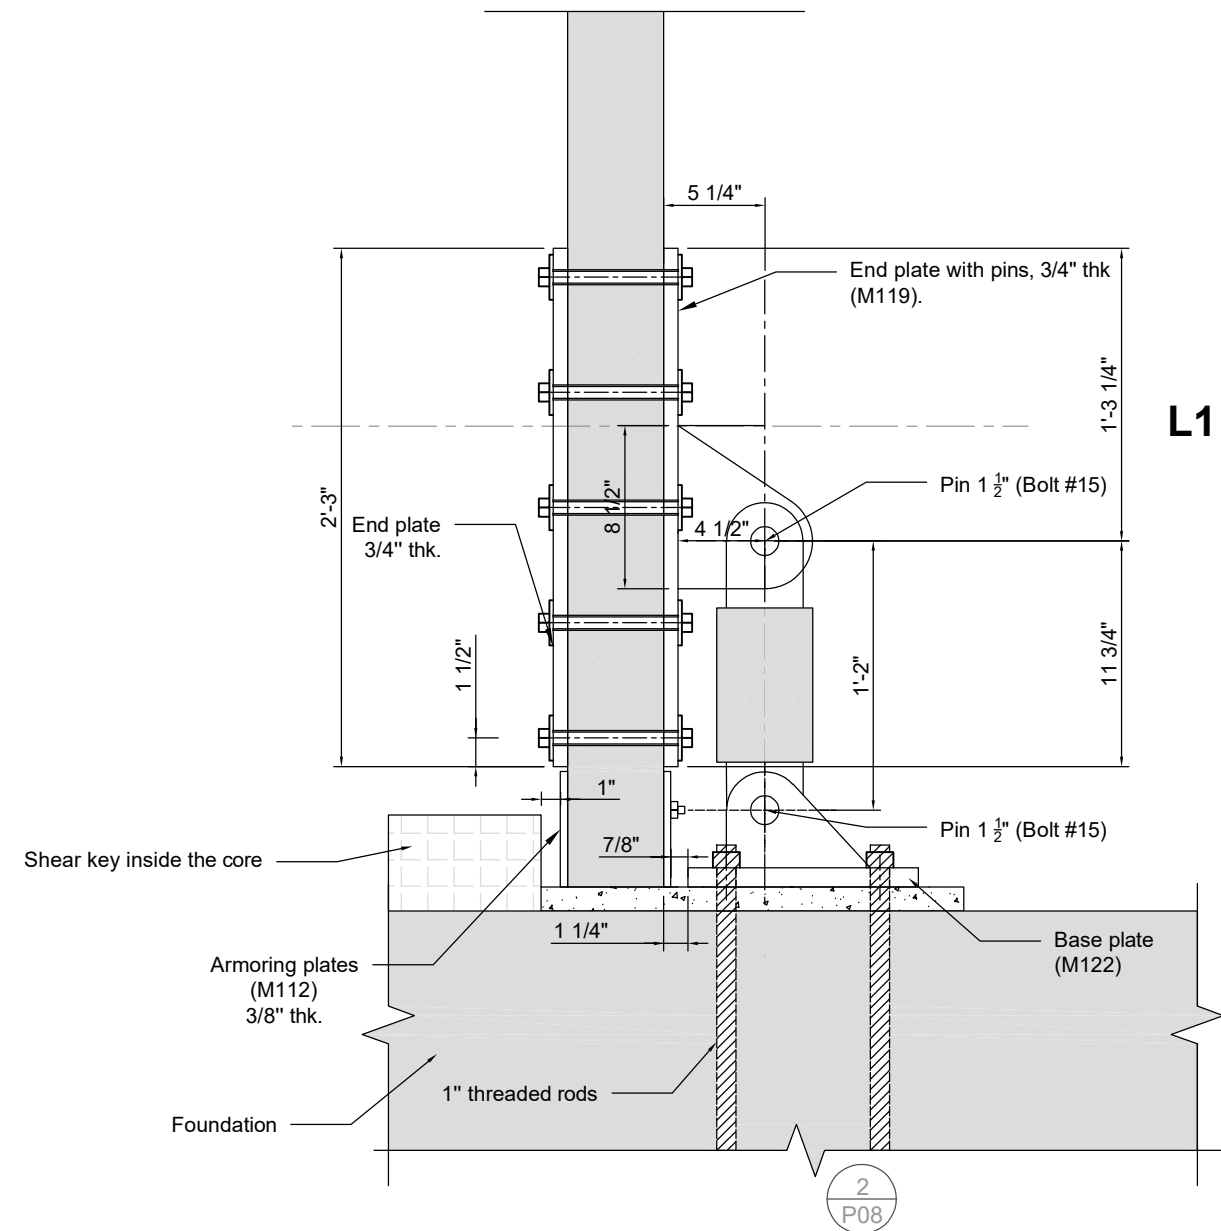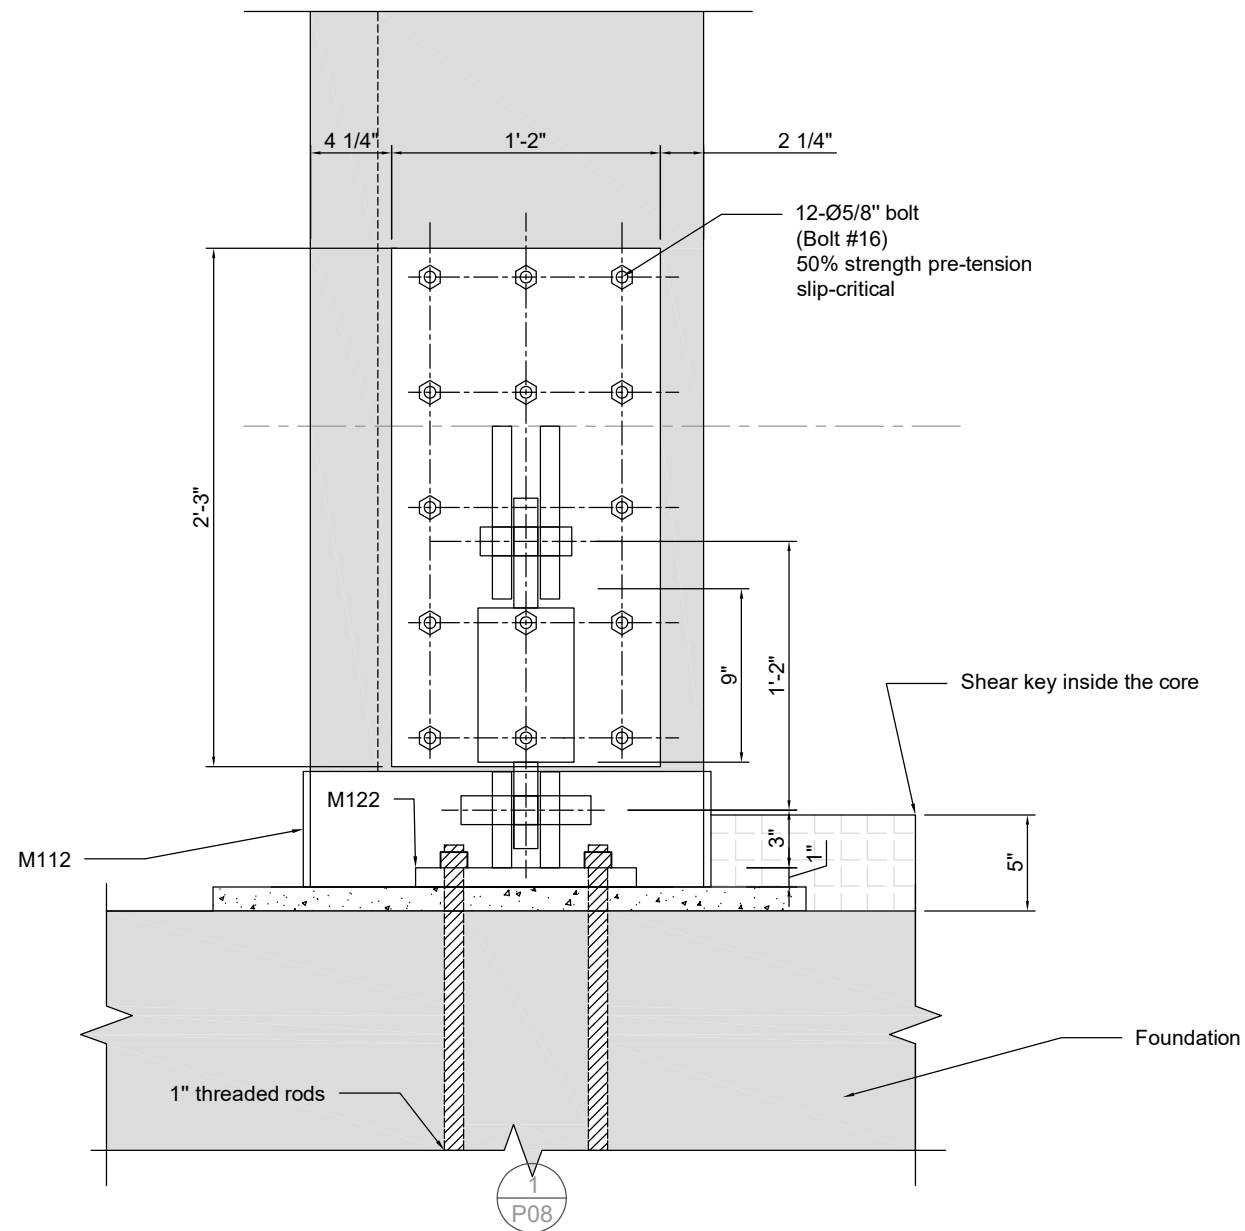

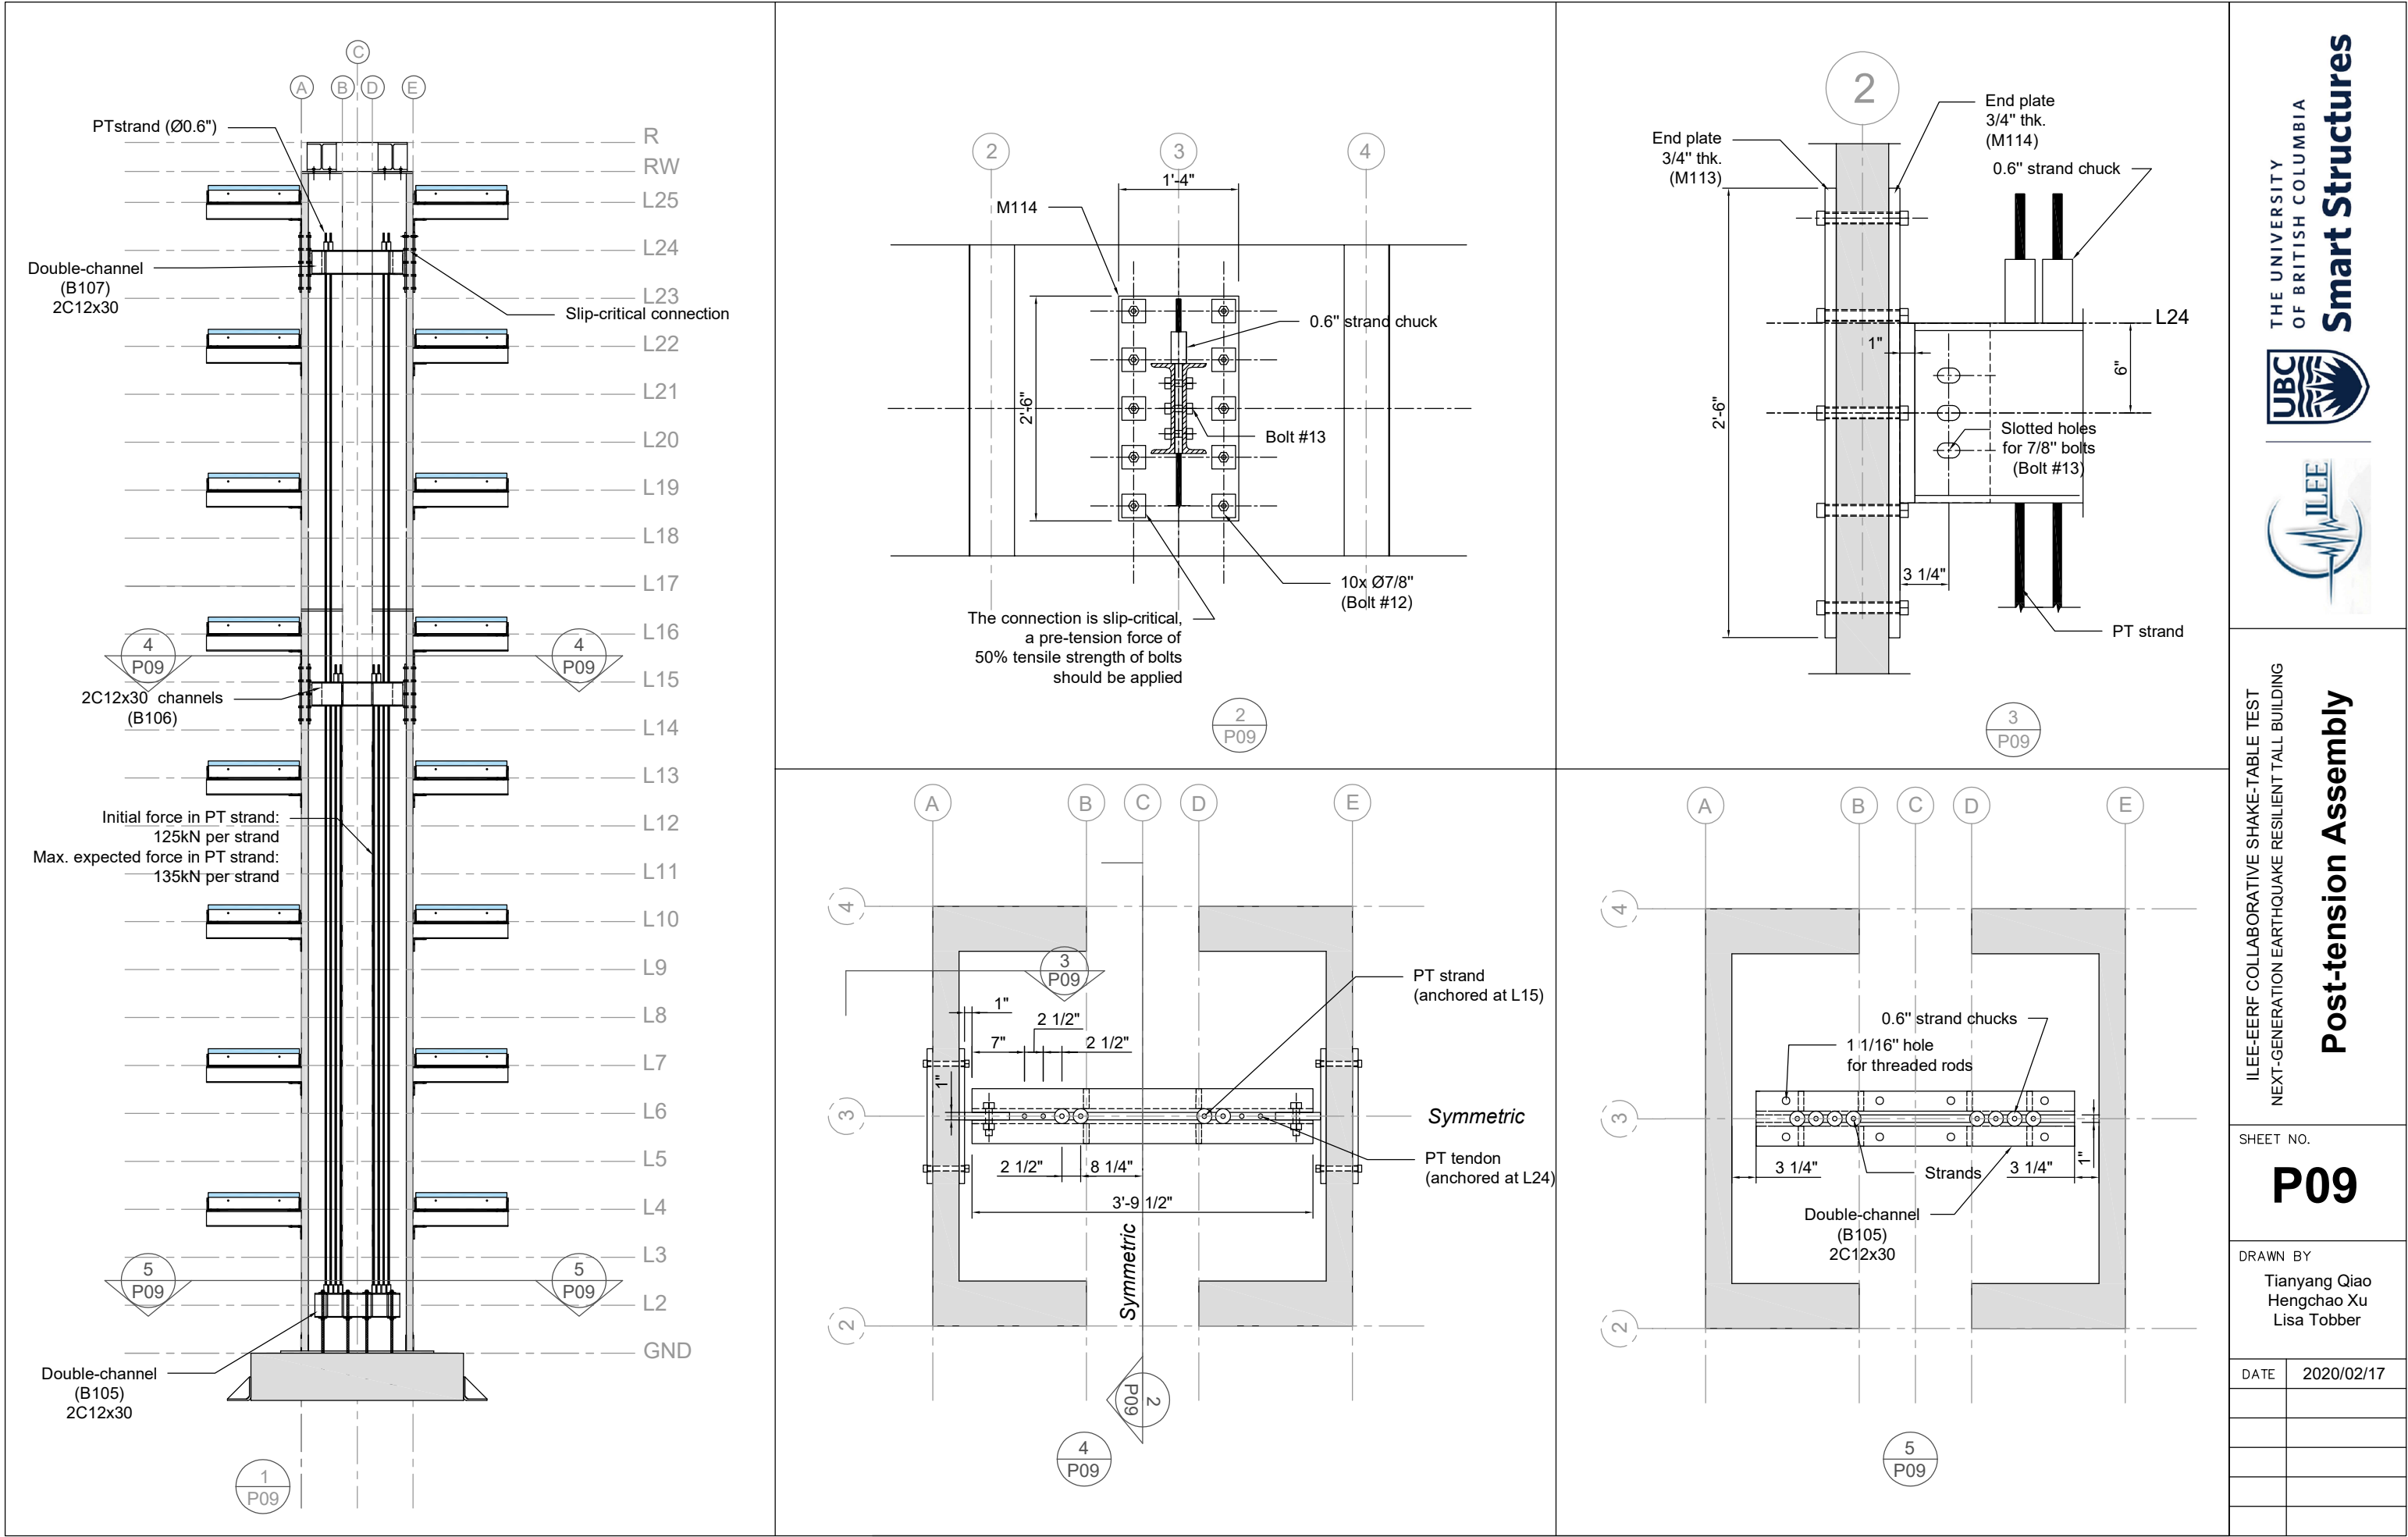

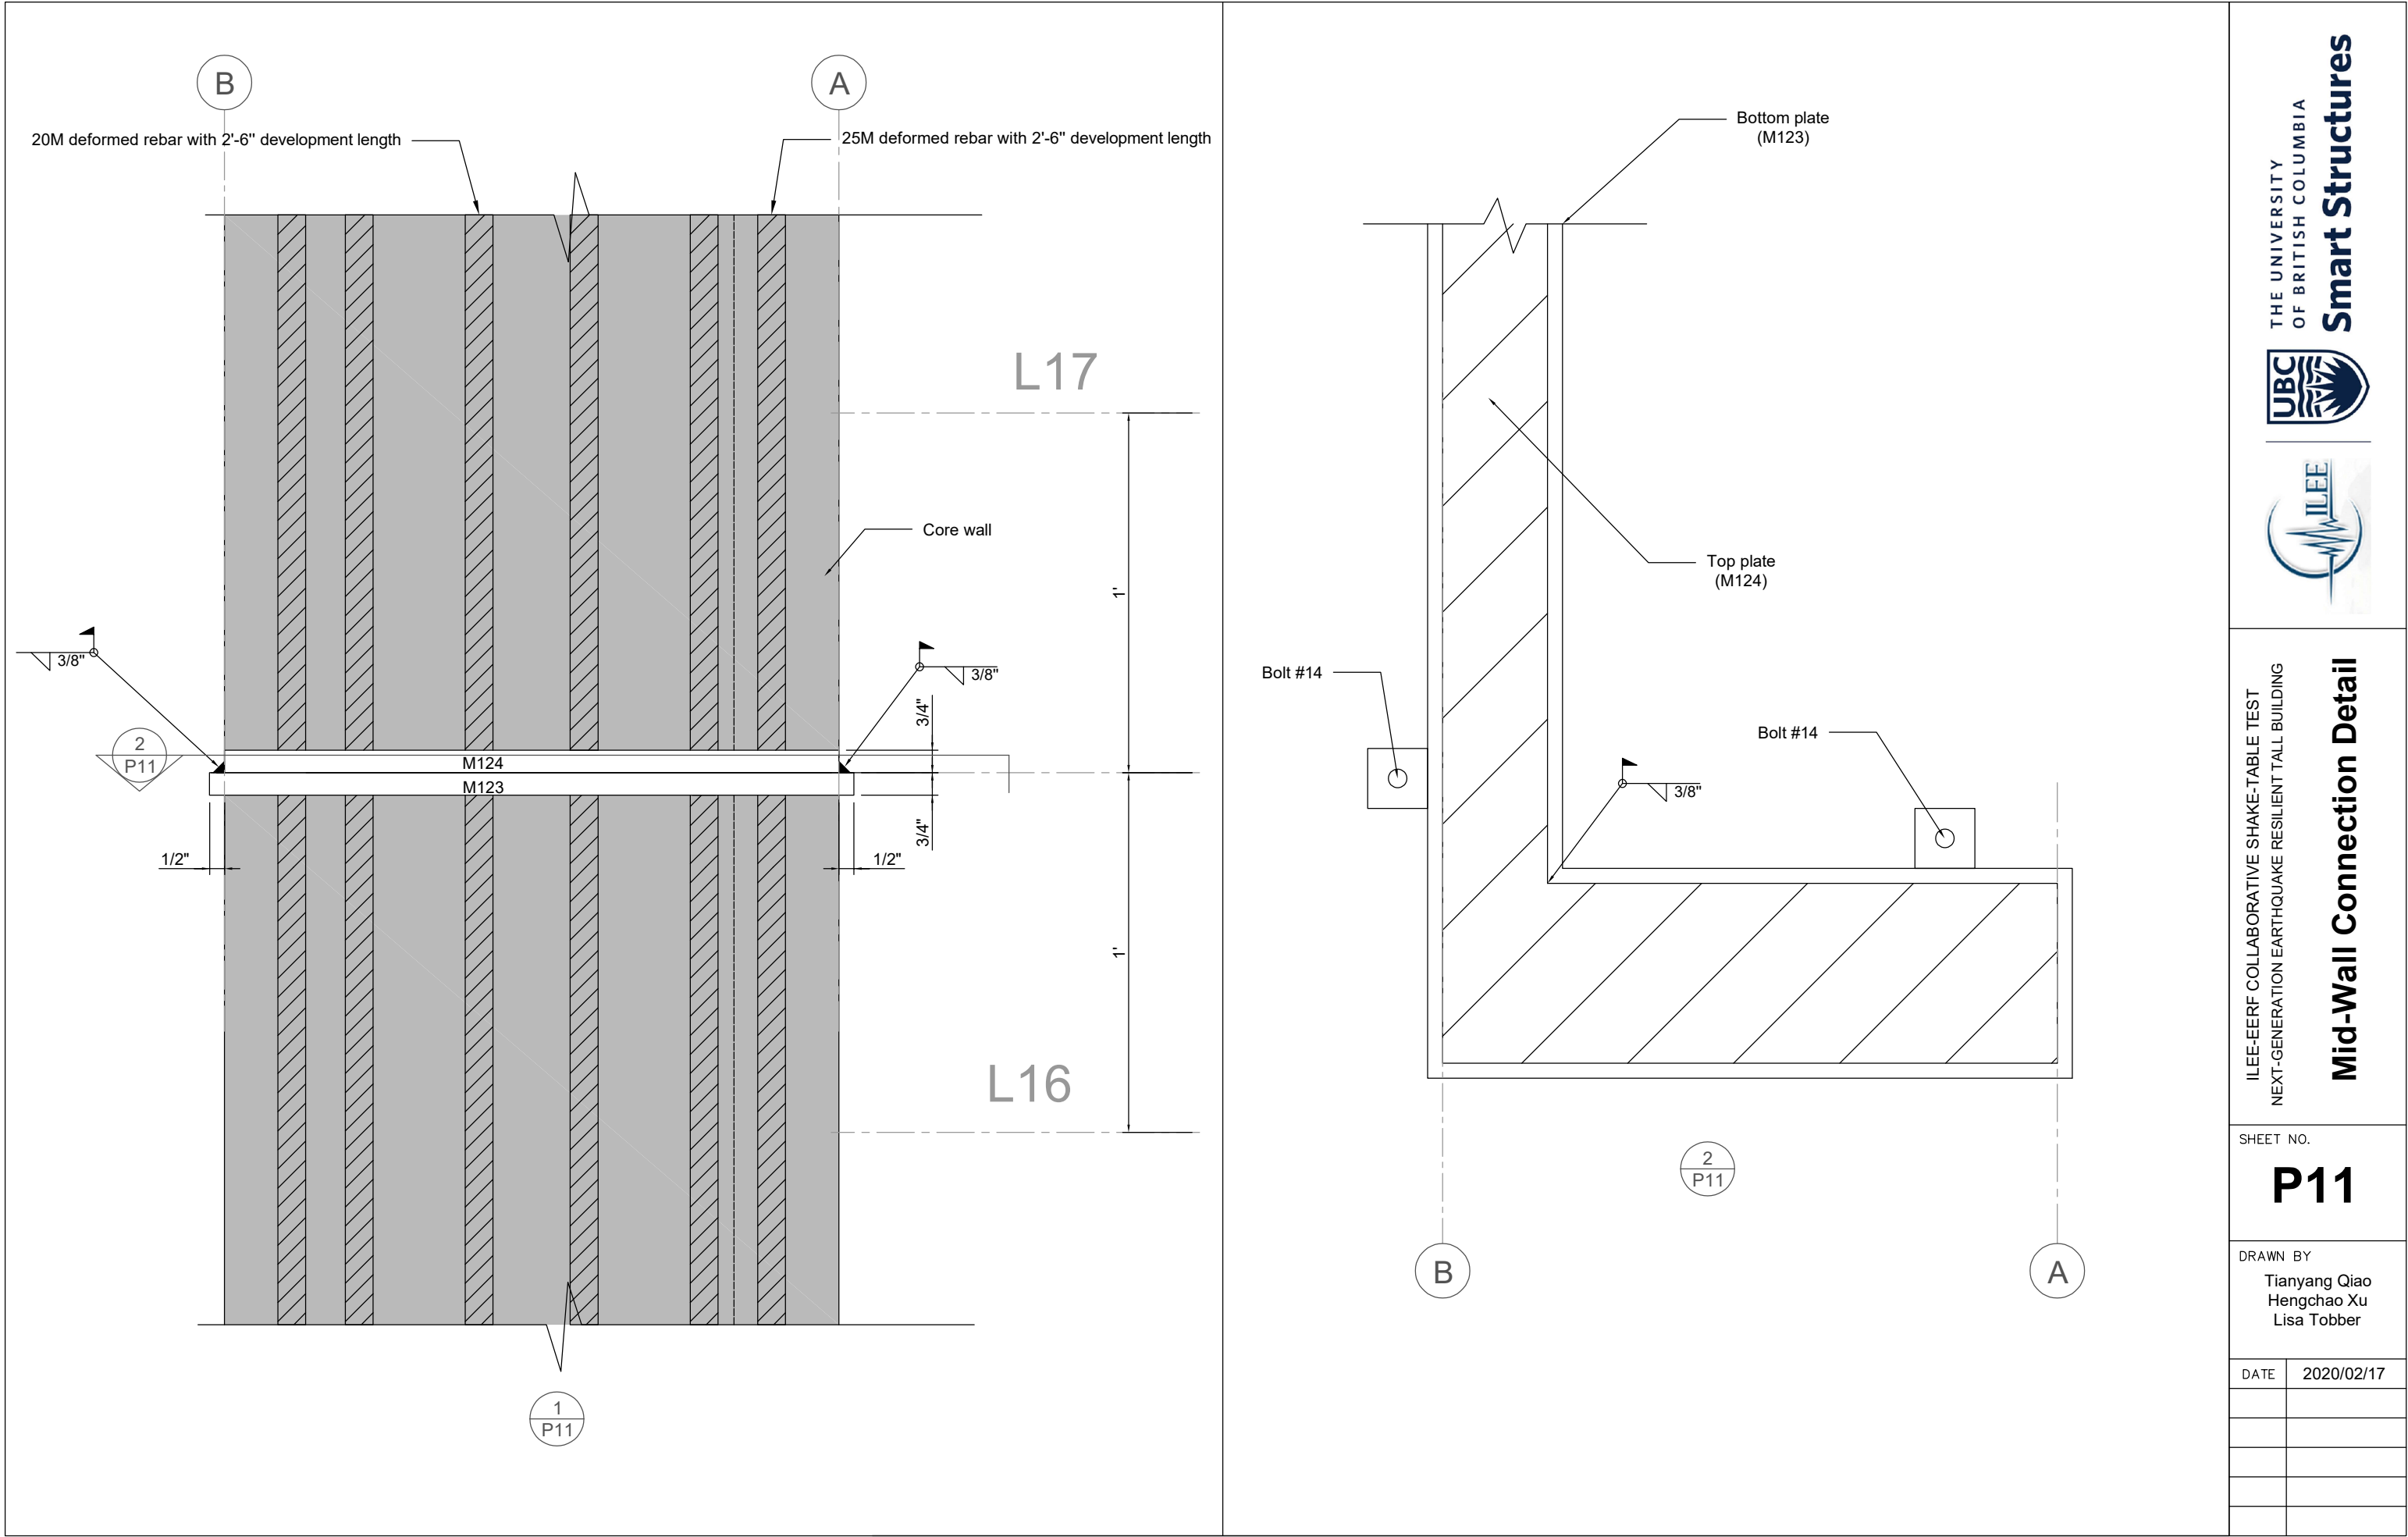

ILEE-EERF COLLABORATIVE SHAKE-TABLE TEST
NEXT-GENERATION EARTHQUAKE RESILIENT TALL BUILDING

SHEET NO.

P11

DRAWN BY
Tianyang Qiao
Hengchao Xu
Lisa Tobber

DATE 2020/02/17