

ILEE-EERF Collaborative Shake Table Test Instrumentation Drawings

Sensor Label		Sensor Types
Type-Level-Component-Grid-Direction/Purpose-#		
D:Displacemnt Gauge (Sp, Lp) A:Accelerometer SG:Strain Gauge LC: Load Pin PG: Pressure Guage MG: MEMS Gyroscope F: Foundation B:Base of the Walls L1-L8:Mass block levels OR: Outrigger level Sht: Shake Table Fnd: Foundation Wall: Wall Beam: Beam Col: Column CB: Coupling Beam Core: Core W2W: Wall to Wall (welding) A:E 1:5 NS EW V: vertical top: top bot: bottom up: uplift slip: slip dist: distortion PT: post-tensioning		Accelerometer
		Strain gauge
		Linear Pot
		String Pot
		Load pin
		Reference on table
		Reference off table
		Donut load cell
		Pressure guage
		MEMS Gyroscope
Table of Contents		Smart Aggregate
Base floor plan: Global Dis of walls & PGs1	Grid 4 elevation: East CBs Strain gauges and Dis.....7	
Below mass blocks 1-4 plan: Global Dis of walls.....2	CB levels plan: Coupling Beams Strain gauges and Dis.....8	
Below mass blocks 5-8 plan: Global Dis and Acc of walls.....3	Outrigger level: Outrigger beam strain gauges.....9	
Grid A and E elevations: Global Dis and Acc of walls.....4	Outrigger level: Outrigger Damper Force and Dis.....10	
Grid 2 and 4 elevations: Global Dis walls.....5	Base level: Base Damper strain gauges.....11	
Grid 2 elevation: West CB Strain gauges and Dis.....6	L5&L8: PT Donut Load Cells.....12	

THE UNIVERSITY OF BRITISH COLUMBIA

Smart Structures

ILEE-EERF COLLABORATIVE SHAKE-TABLE TEST
NEXT-GENERATION EARTHQUAKE RESILIENT TALL BUILDING

Title Page

SHEET NO.

0

DRAWN BY

Amin Sadeghi
Henry Xu
Lisa Tobber

DATE

Oct-2019

Scale


-





Global Dis
Base of the walls



01

Scale	1:30
-------	------

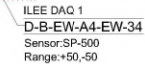

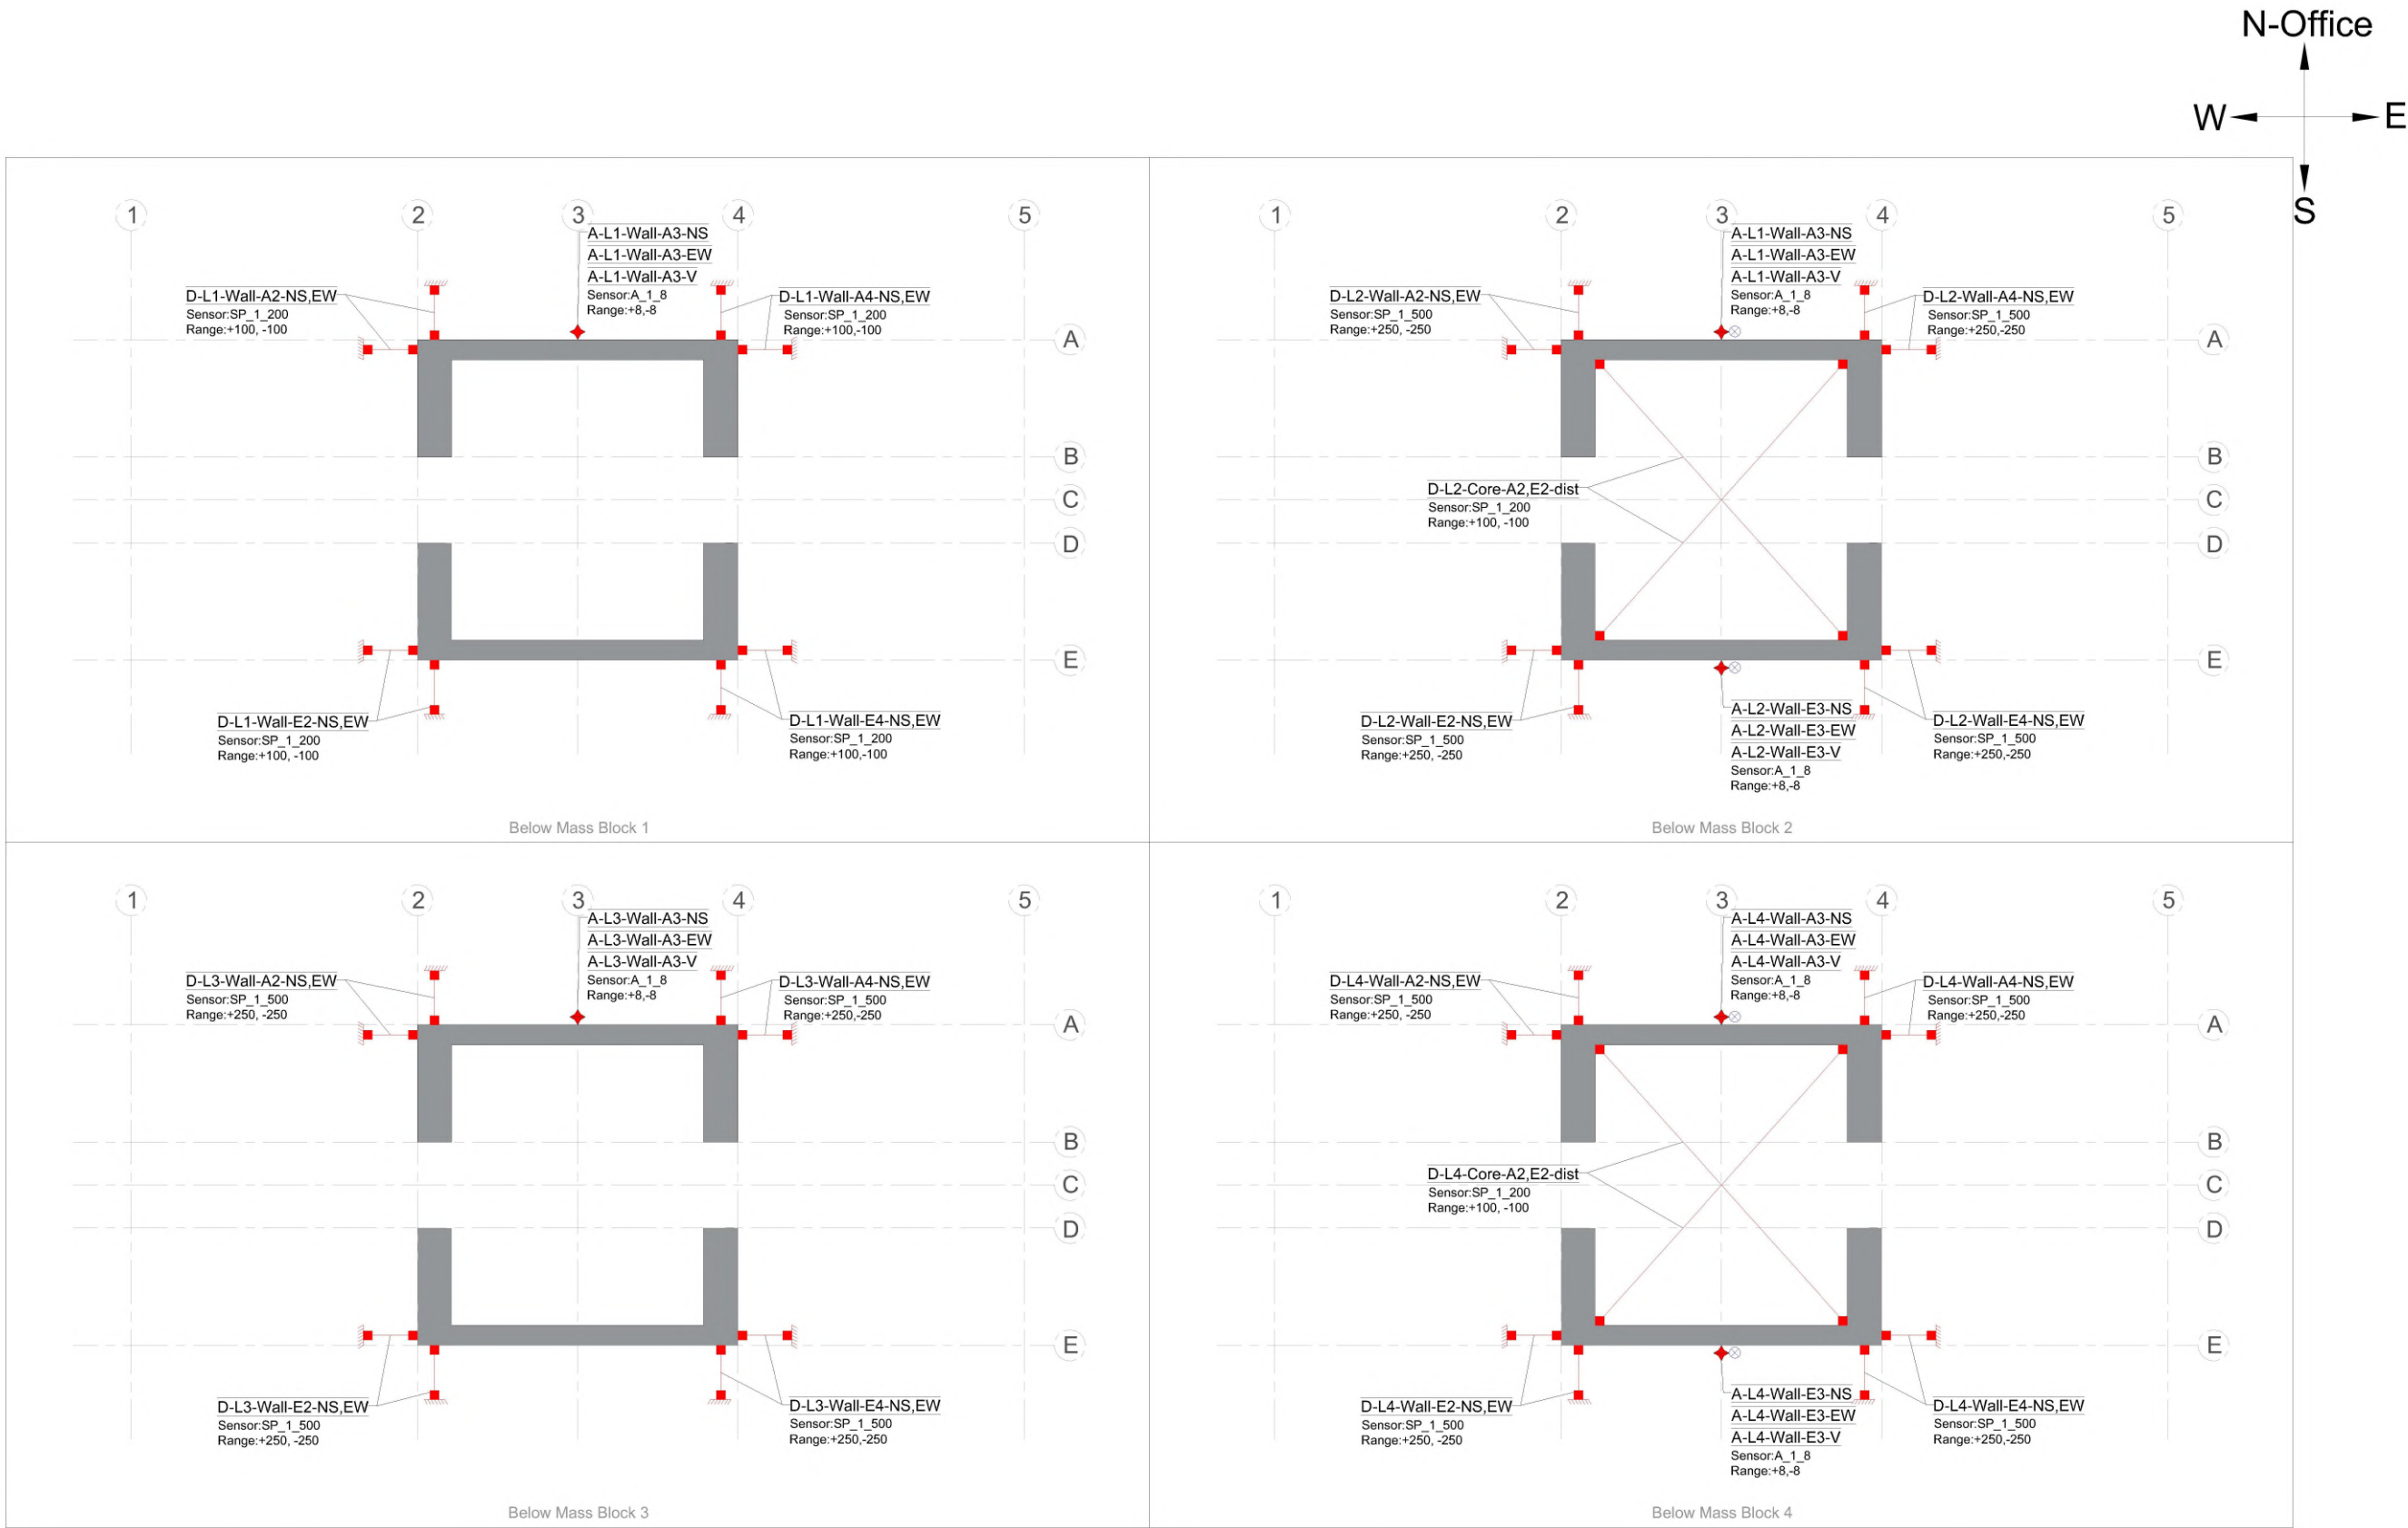

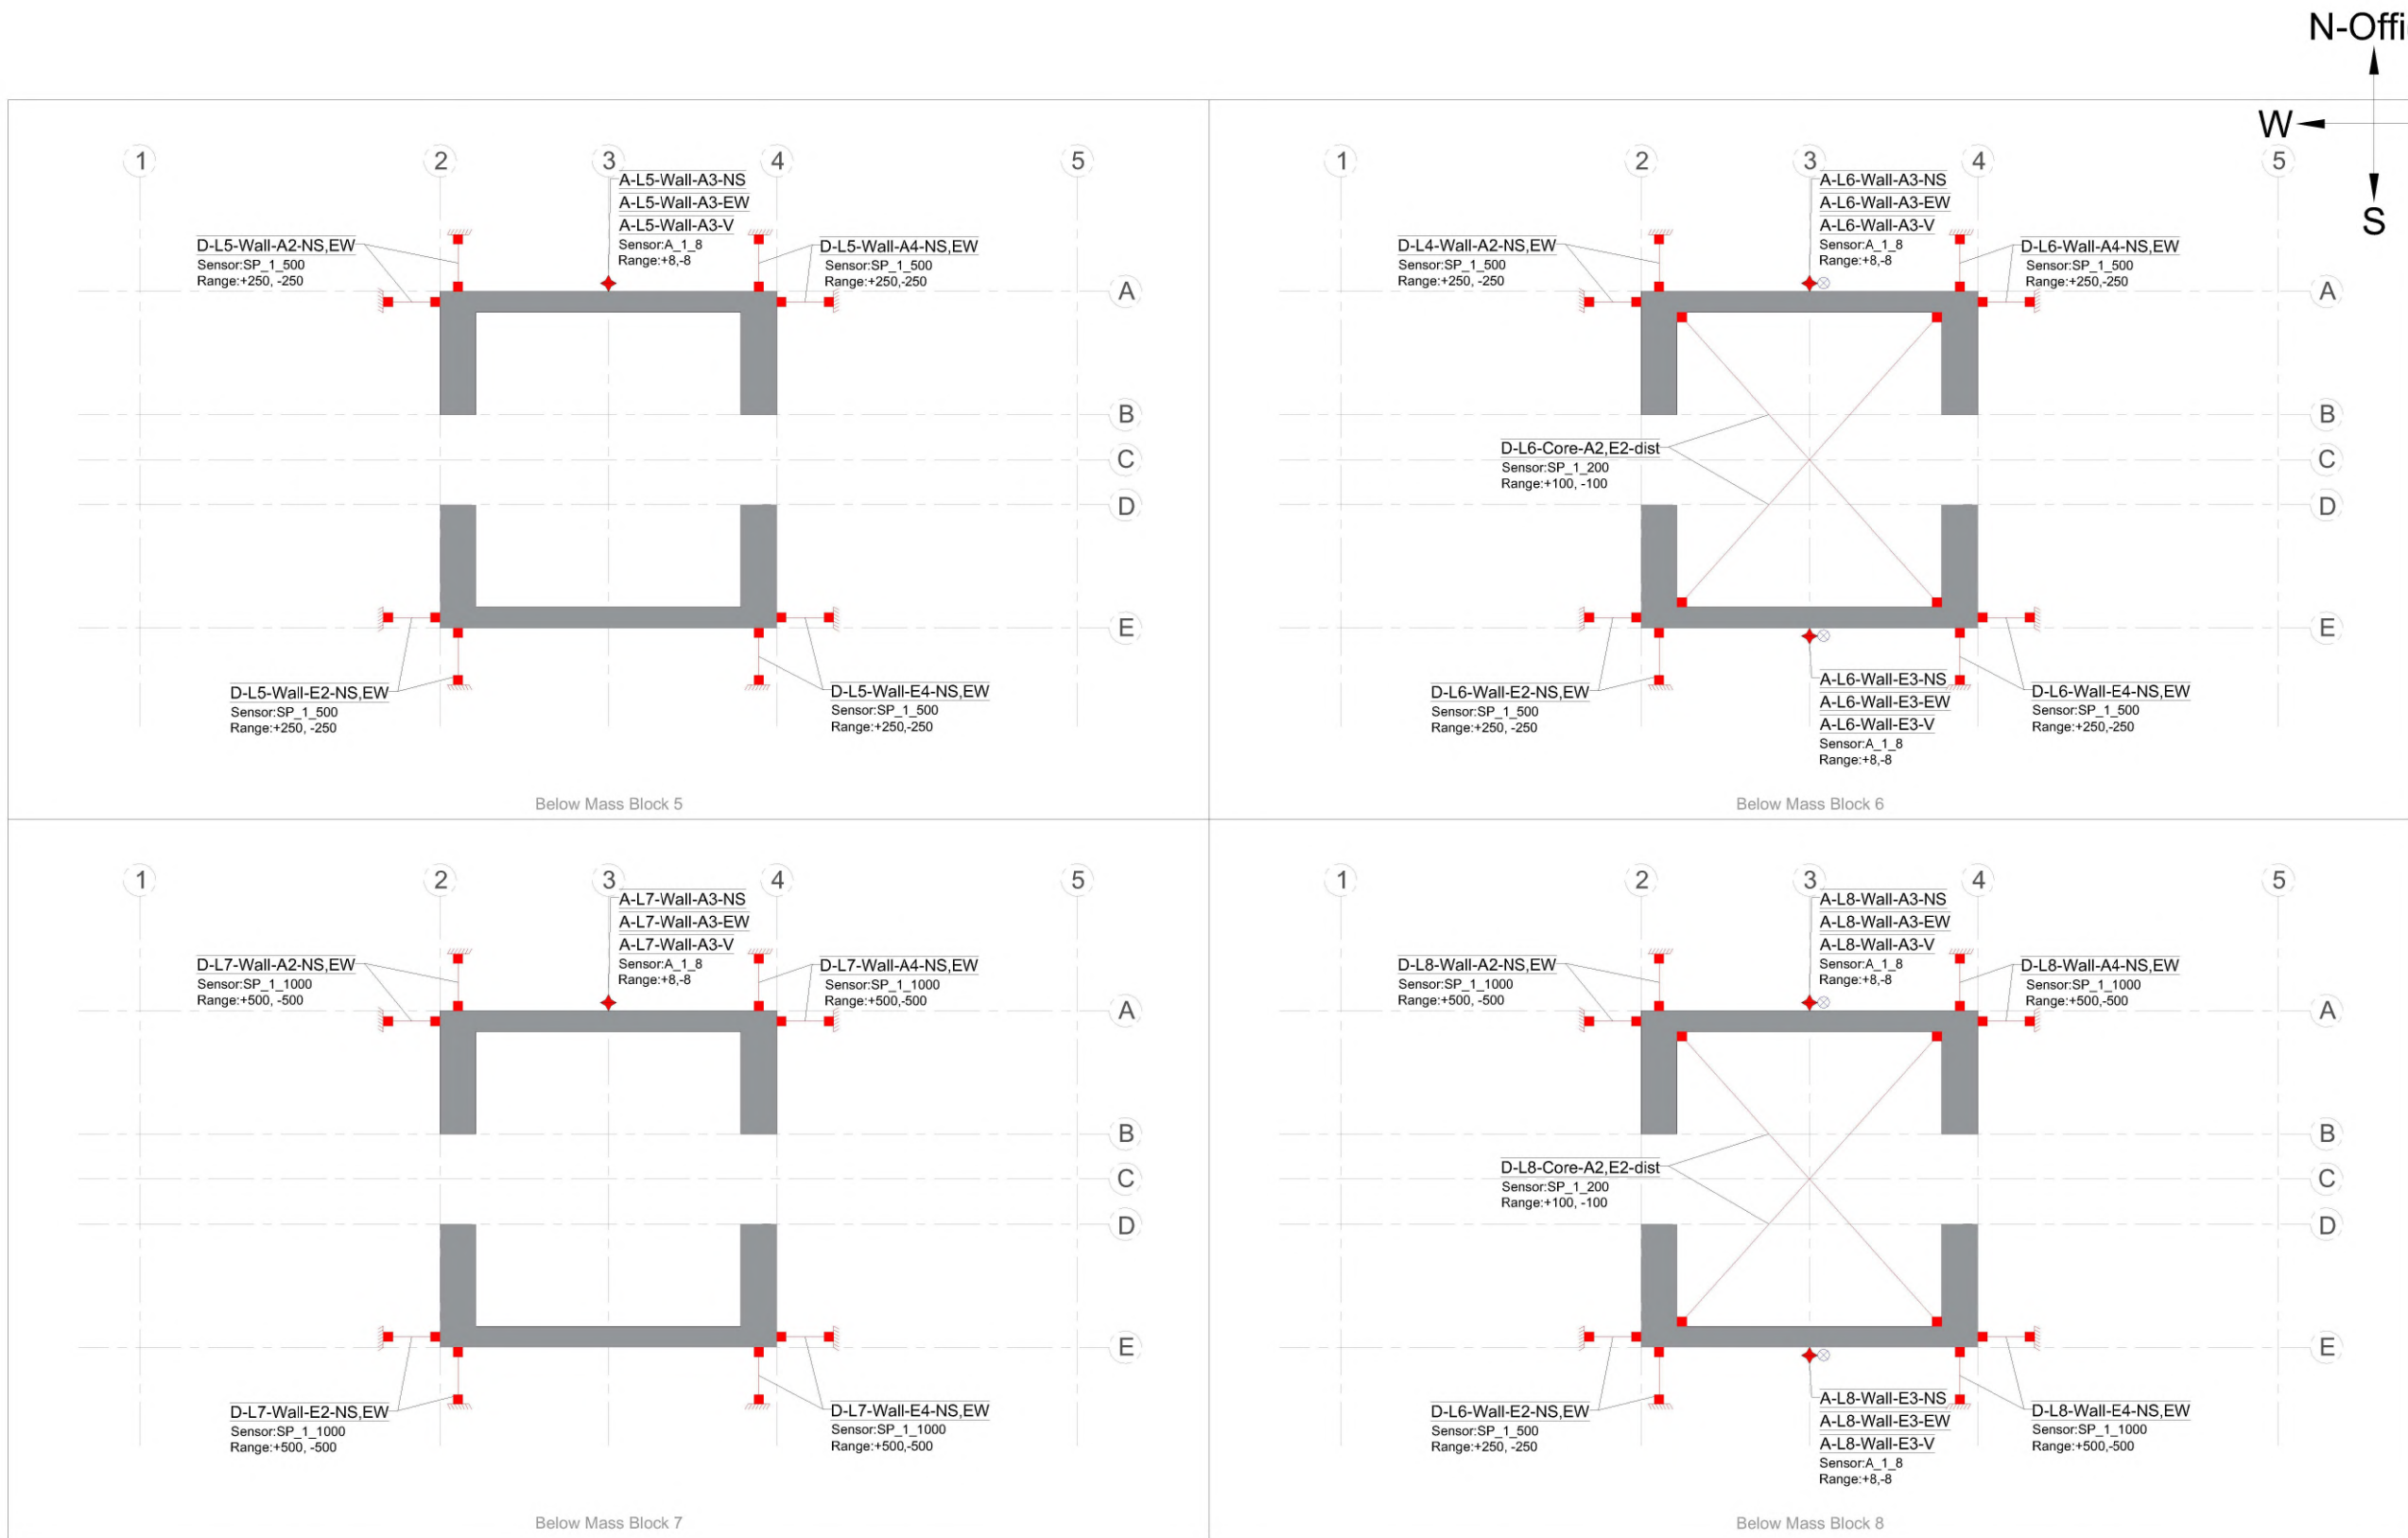

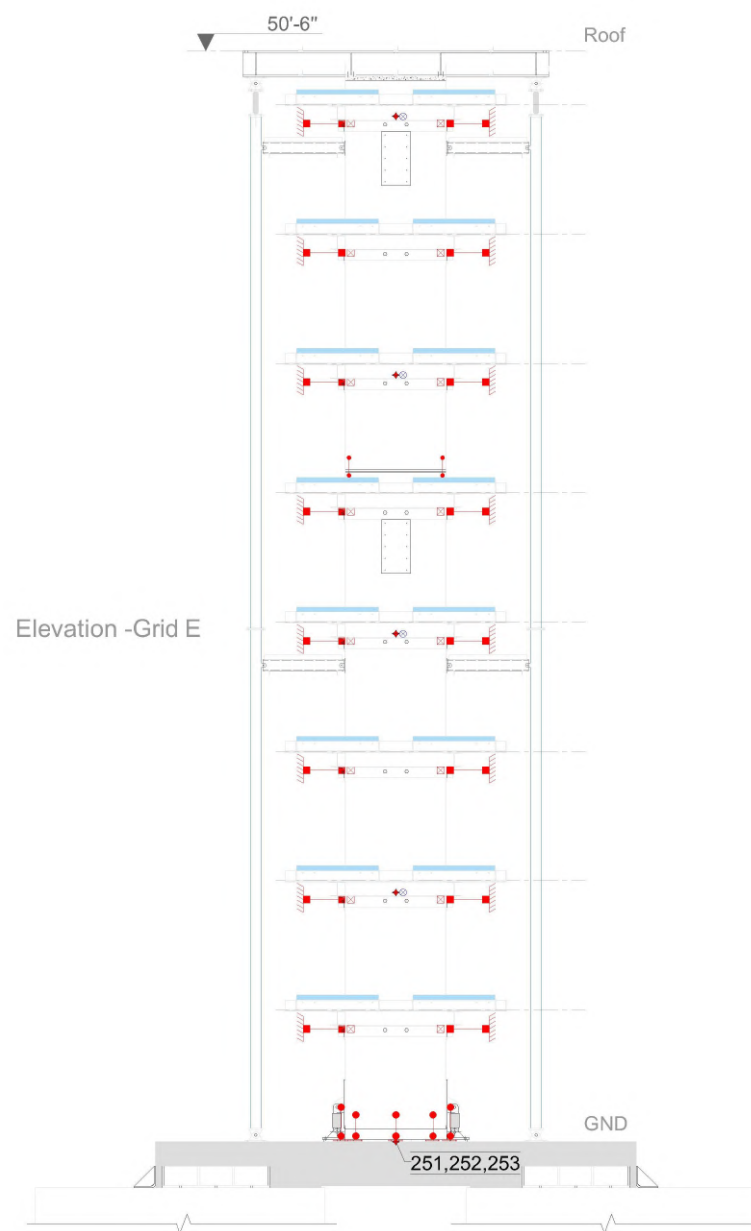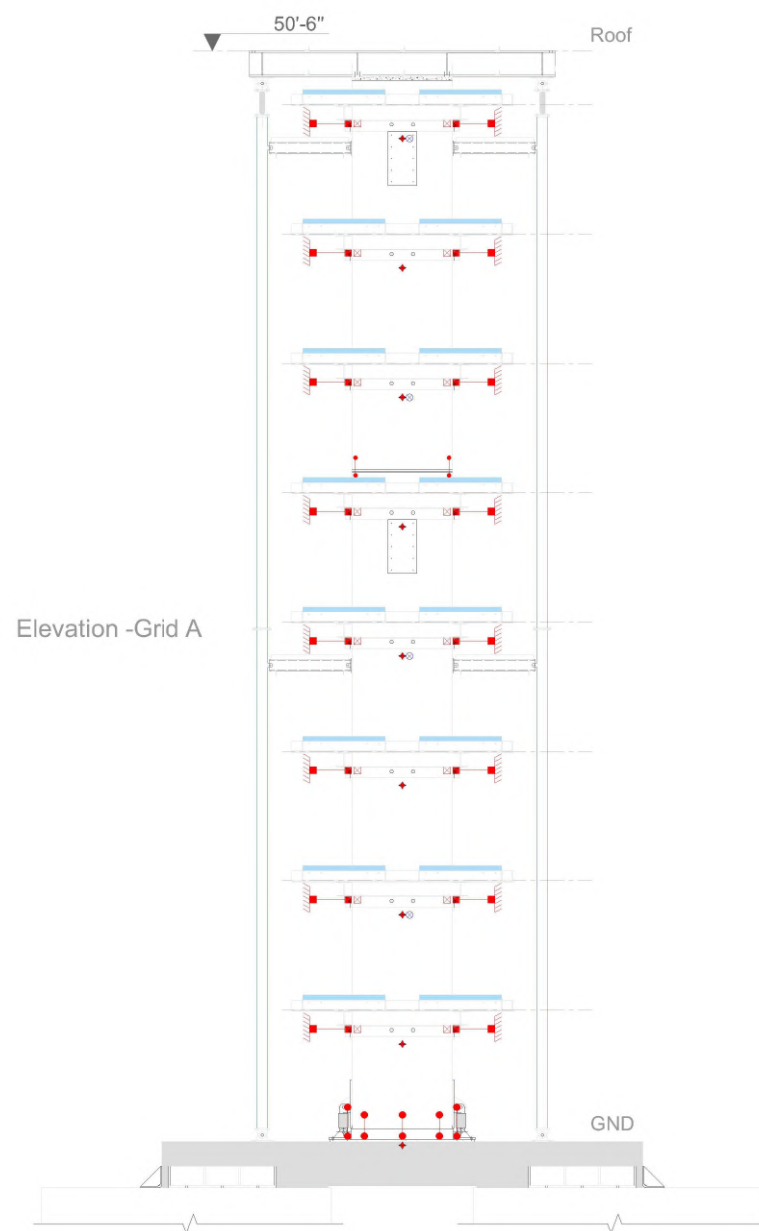

ILEE-EERF COLLABORATIVE SHAKE-TABLE TEST
NEXT-GENERATION EARTHQUAKE RESILIENT TALL BUILDING

Glob Acc and Dis of walls

Elevation-Grid A,E

SHEET NO.

04

DRAWN BY

Amin Sadeghi
Henry Xu
Lisa Tobber

DATE Oct-2019


Scale 1:64






THE UNIVERSITY
OF BRITISH COLUMBIA


Smart Structures




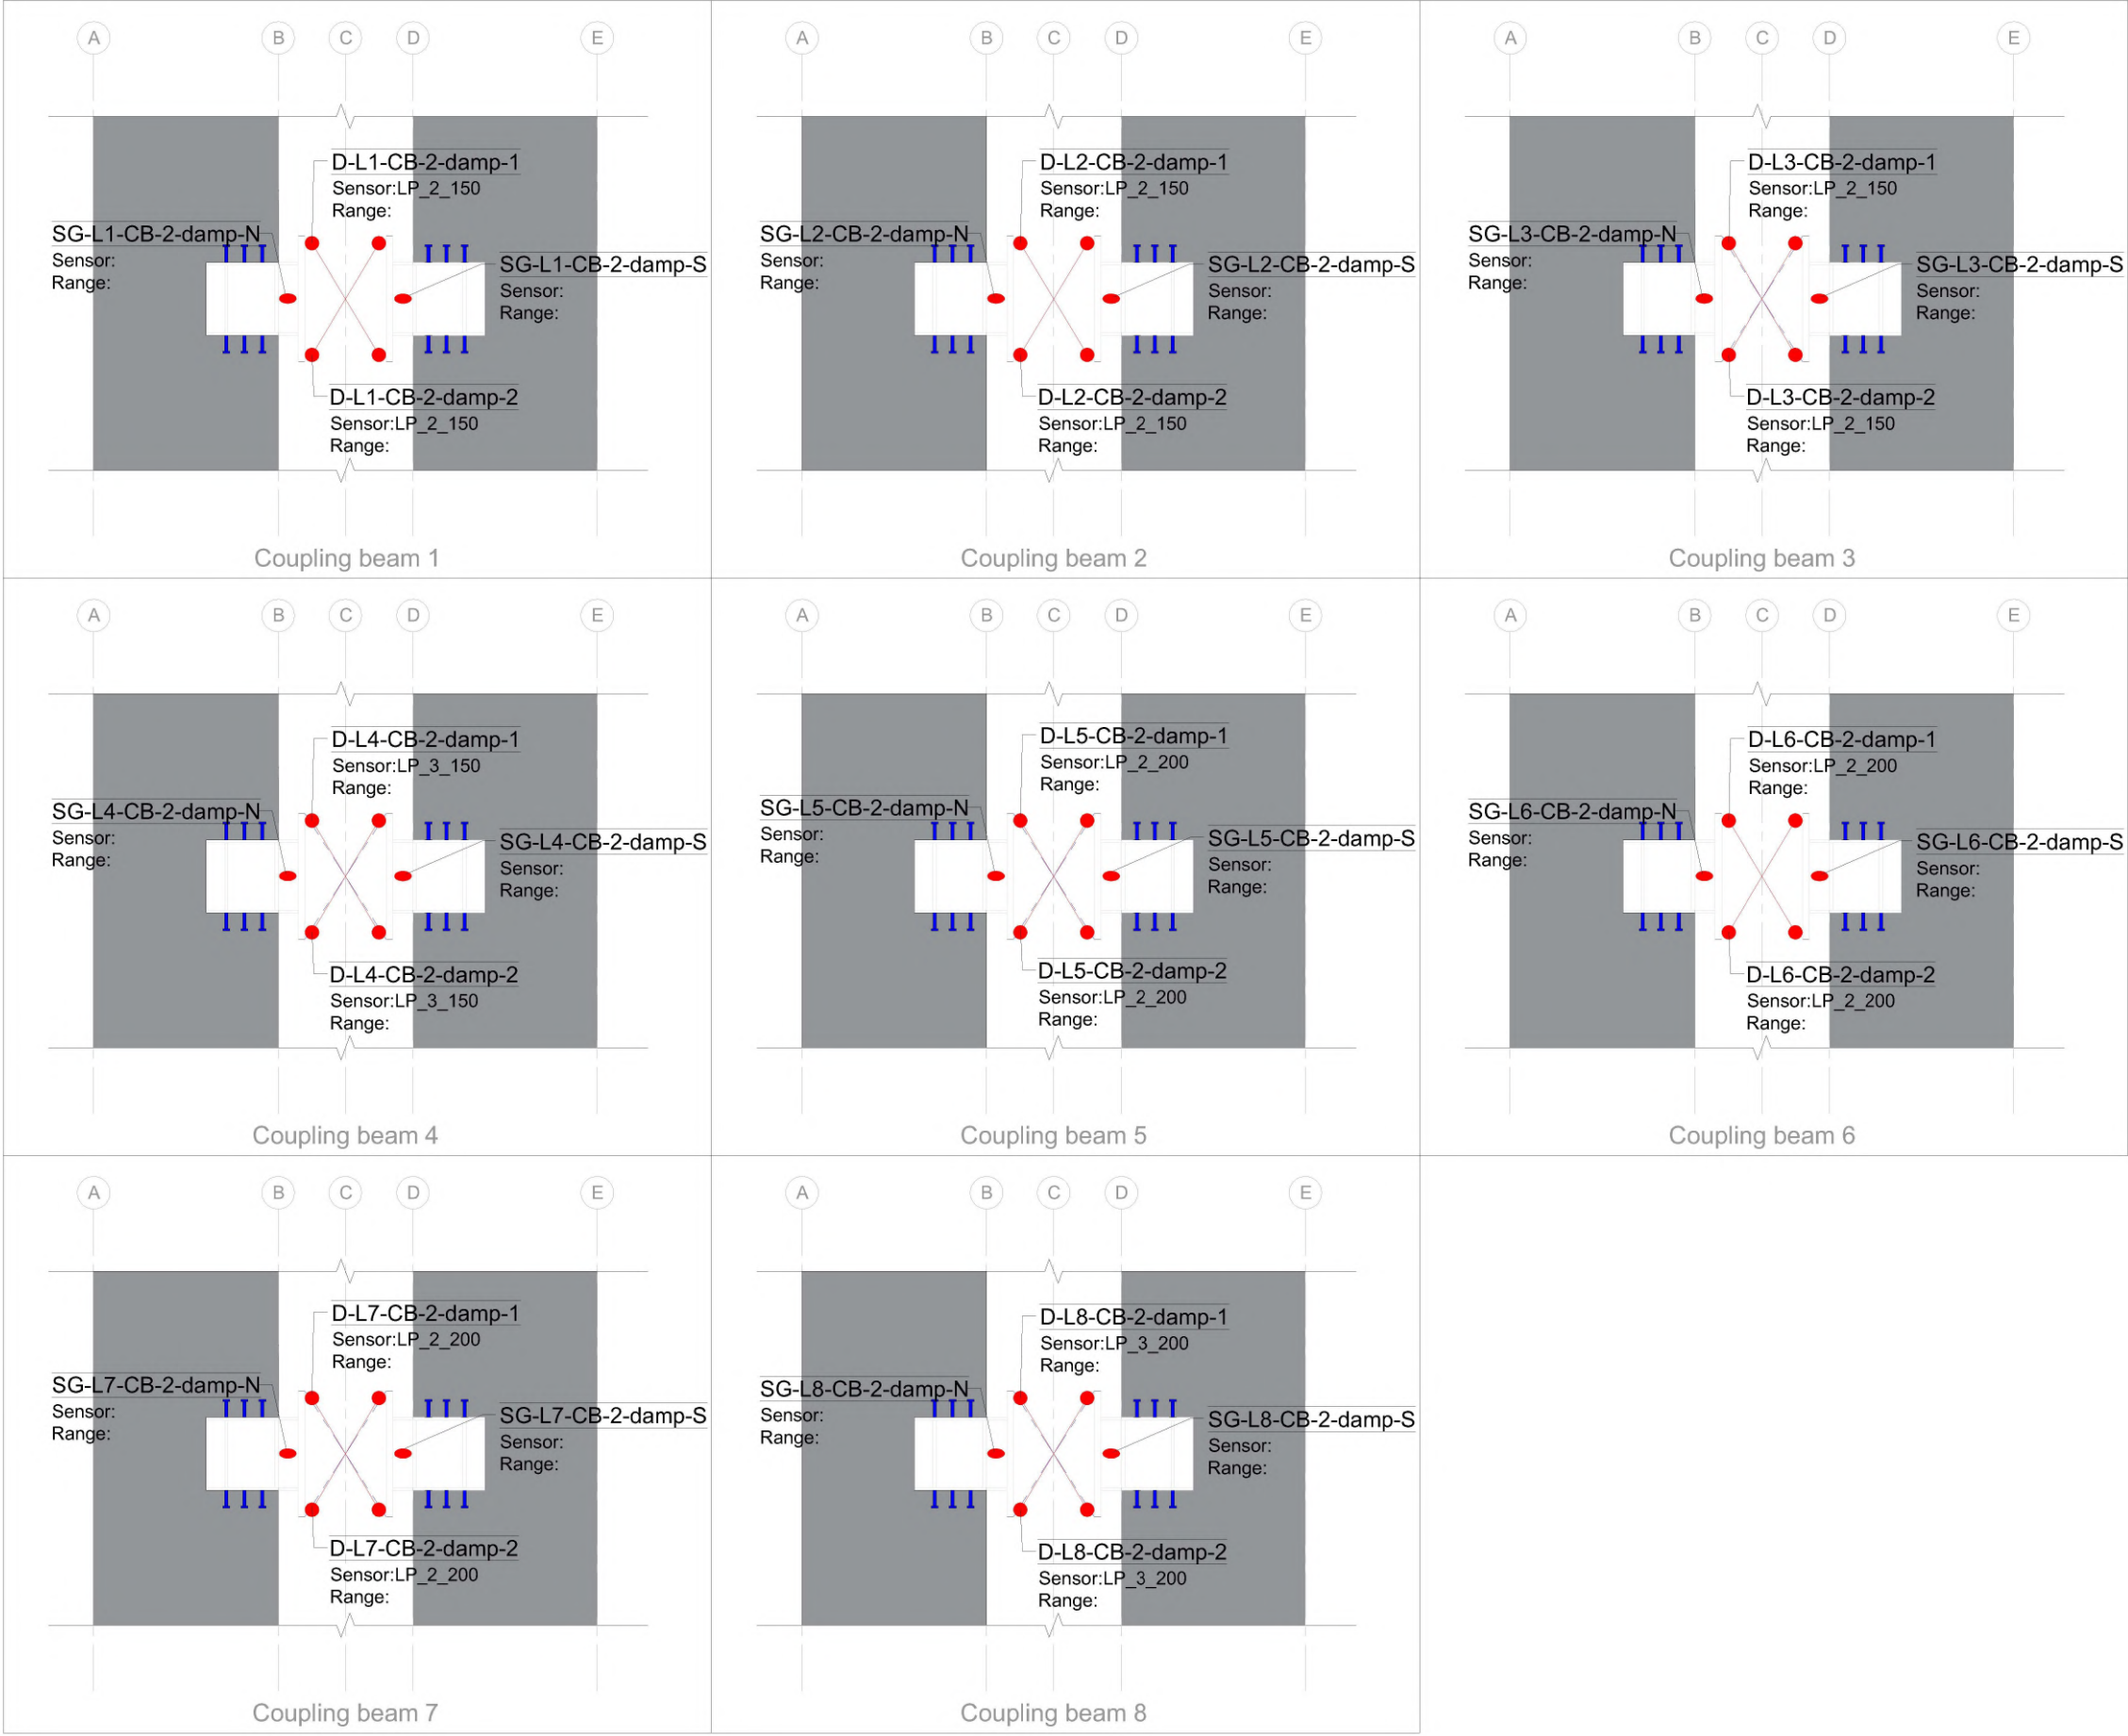

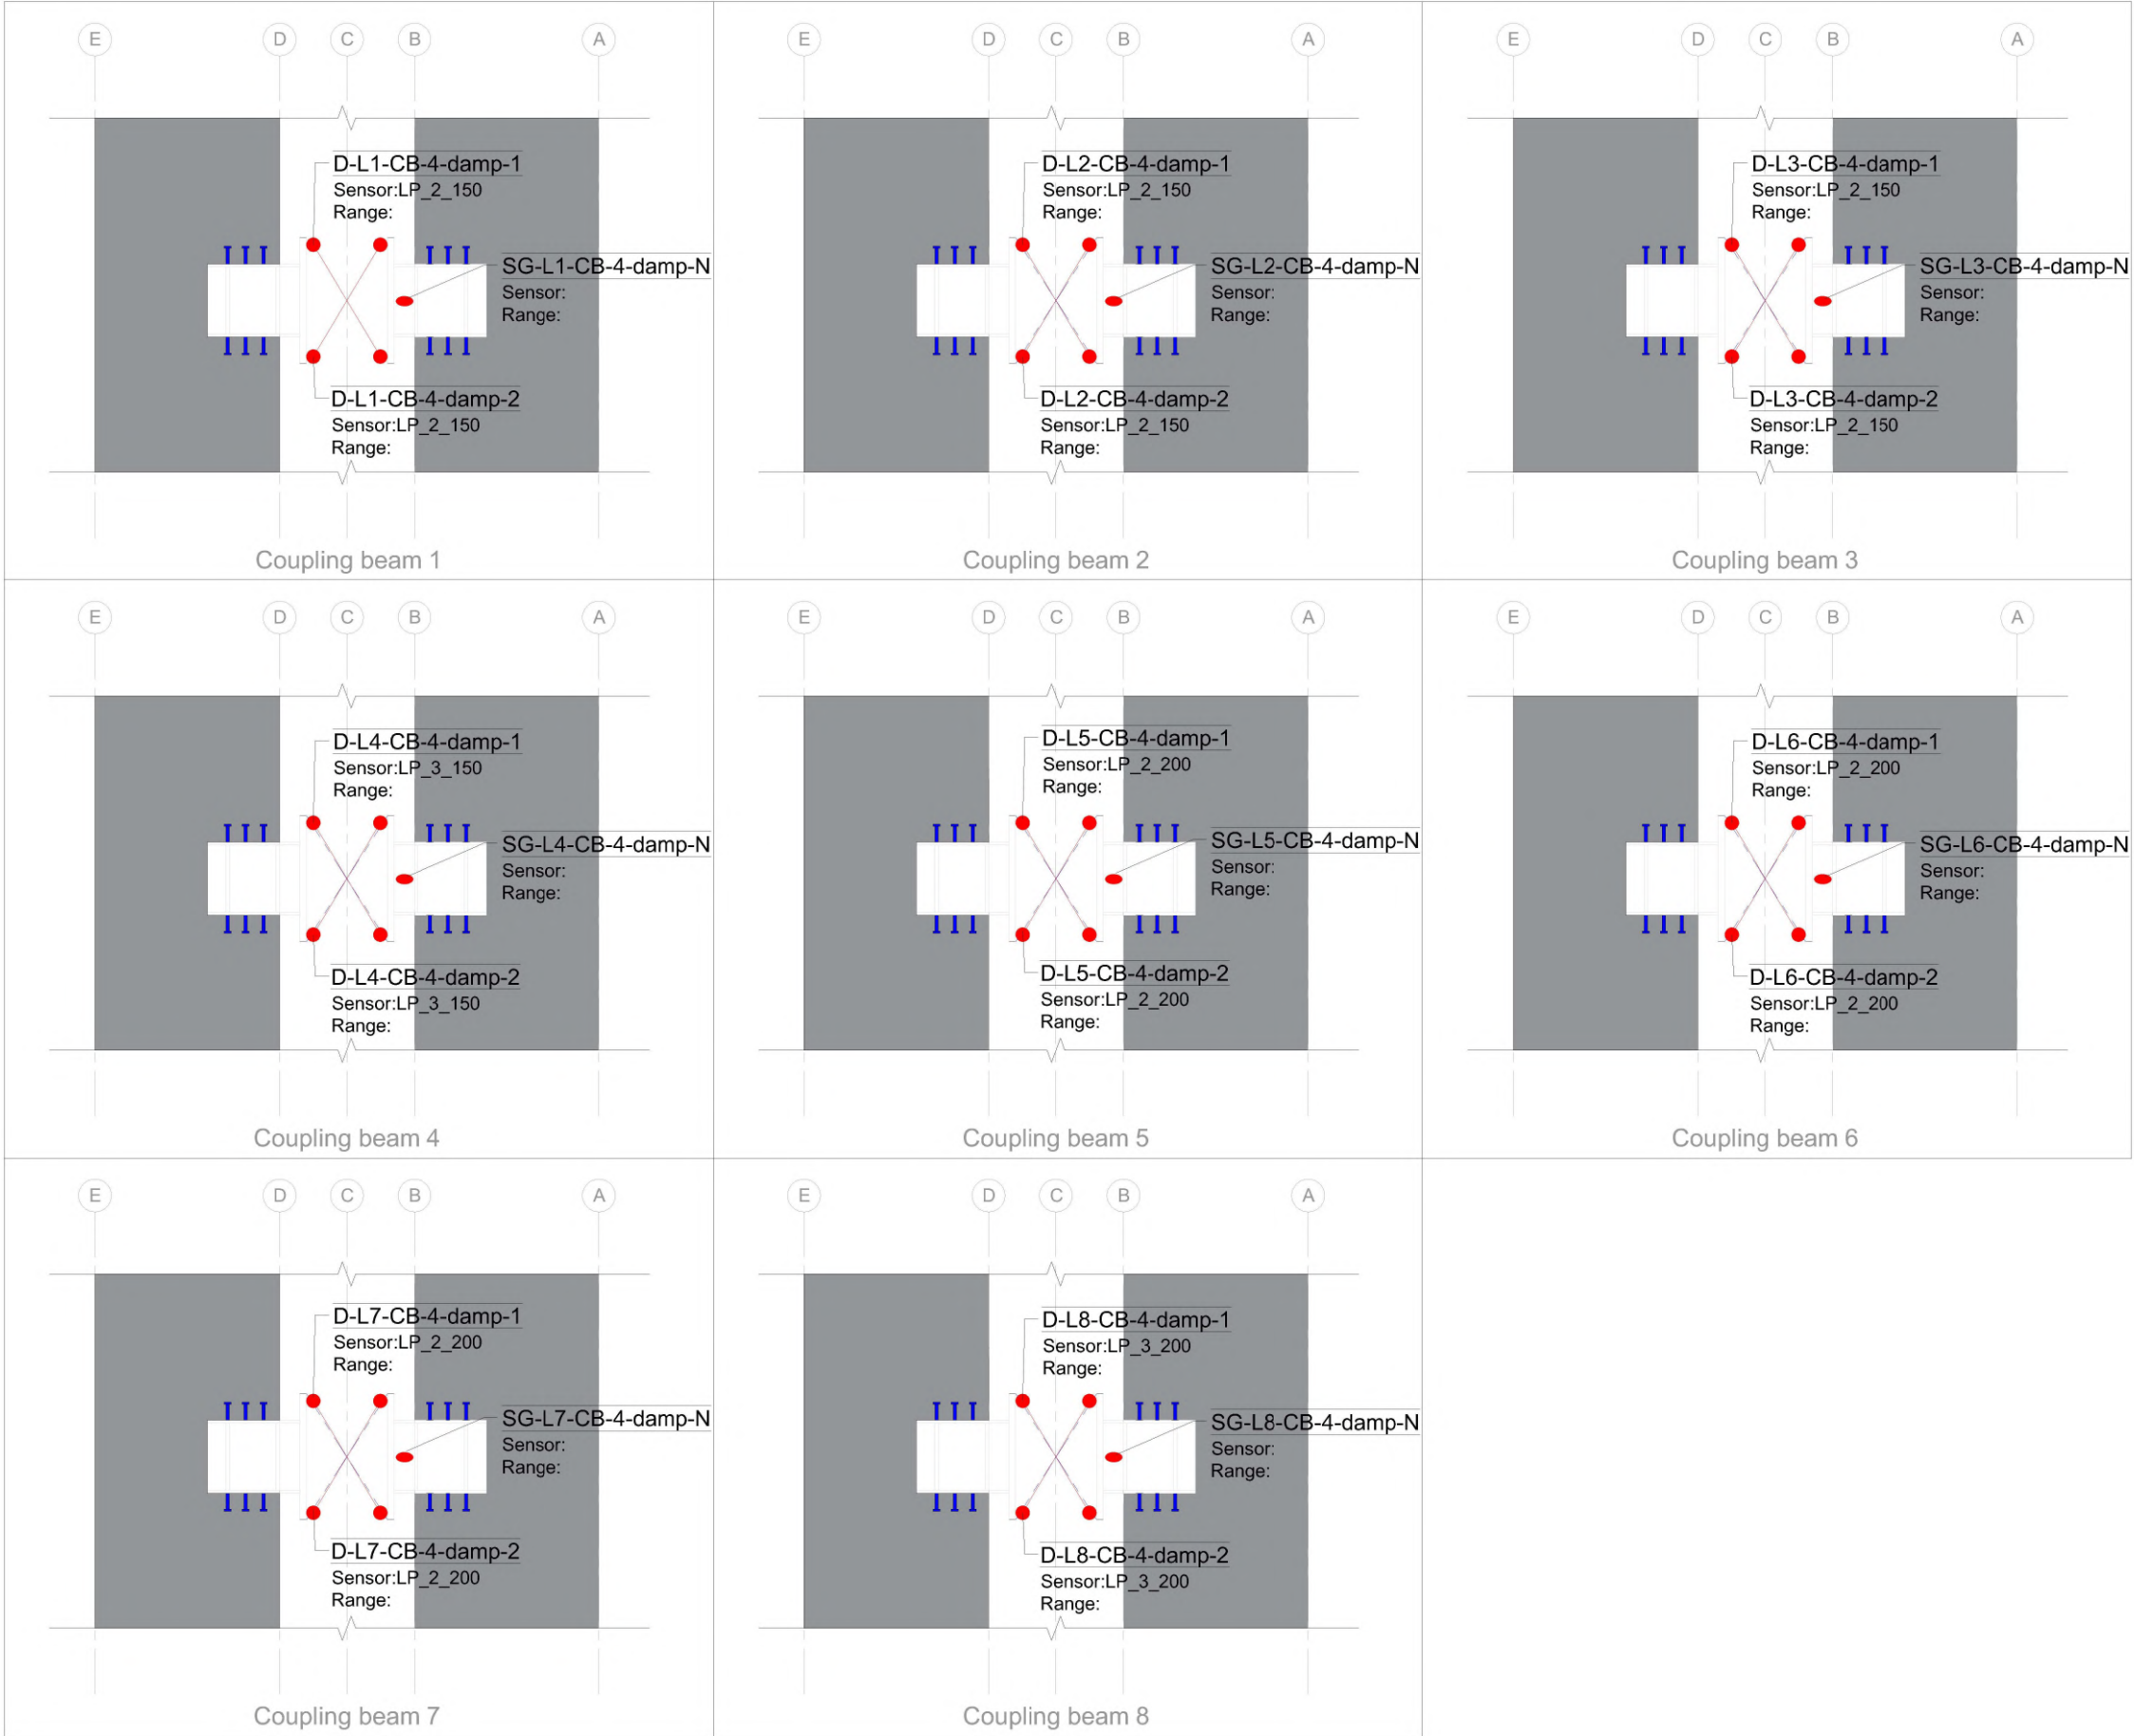


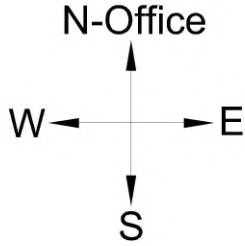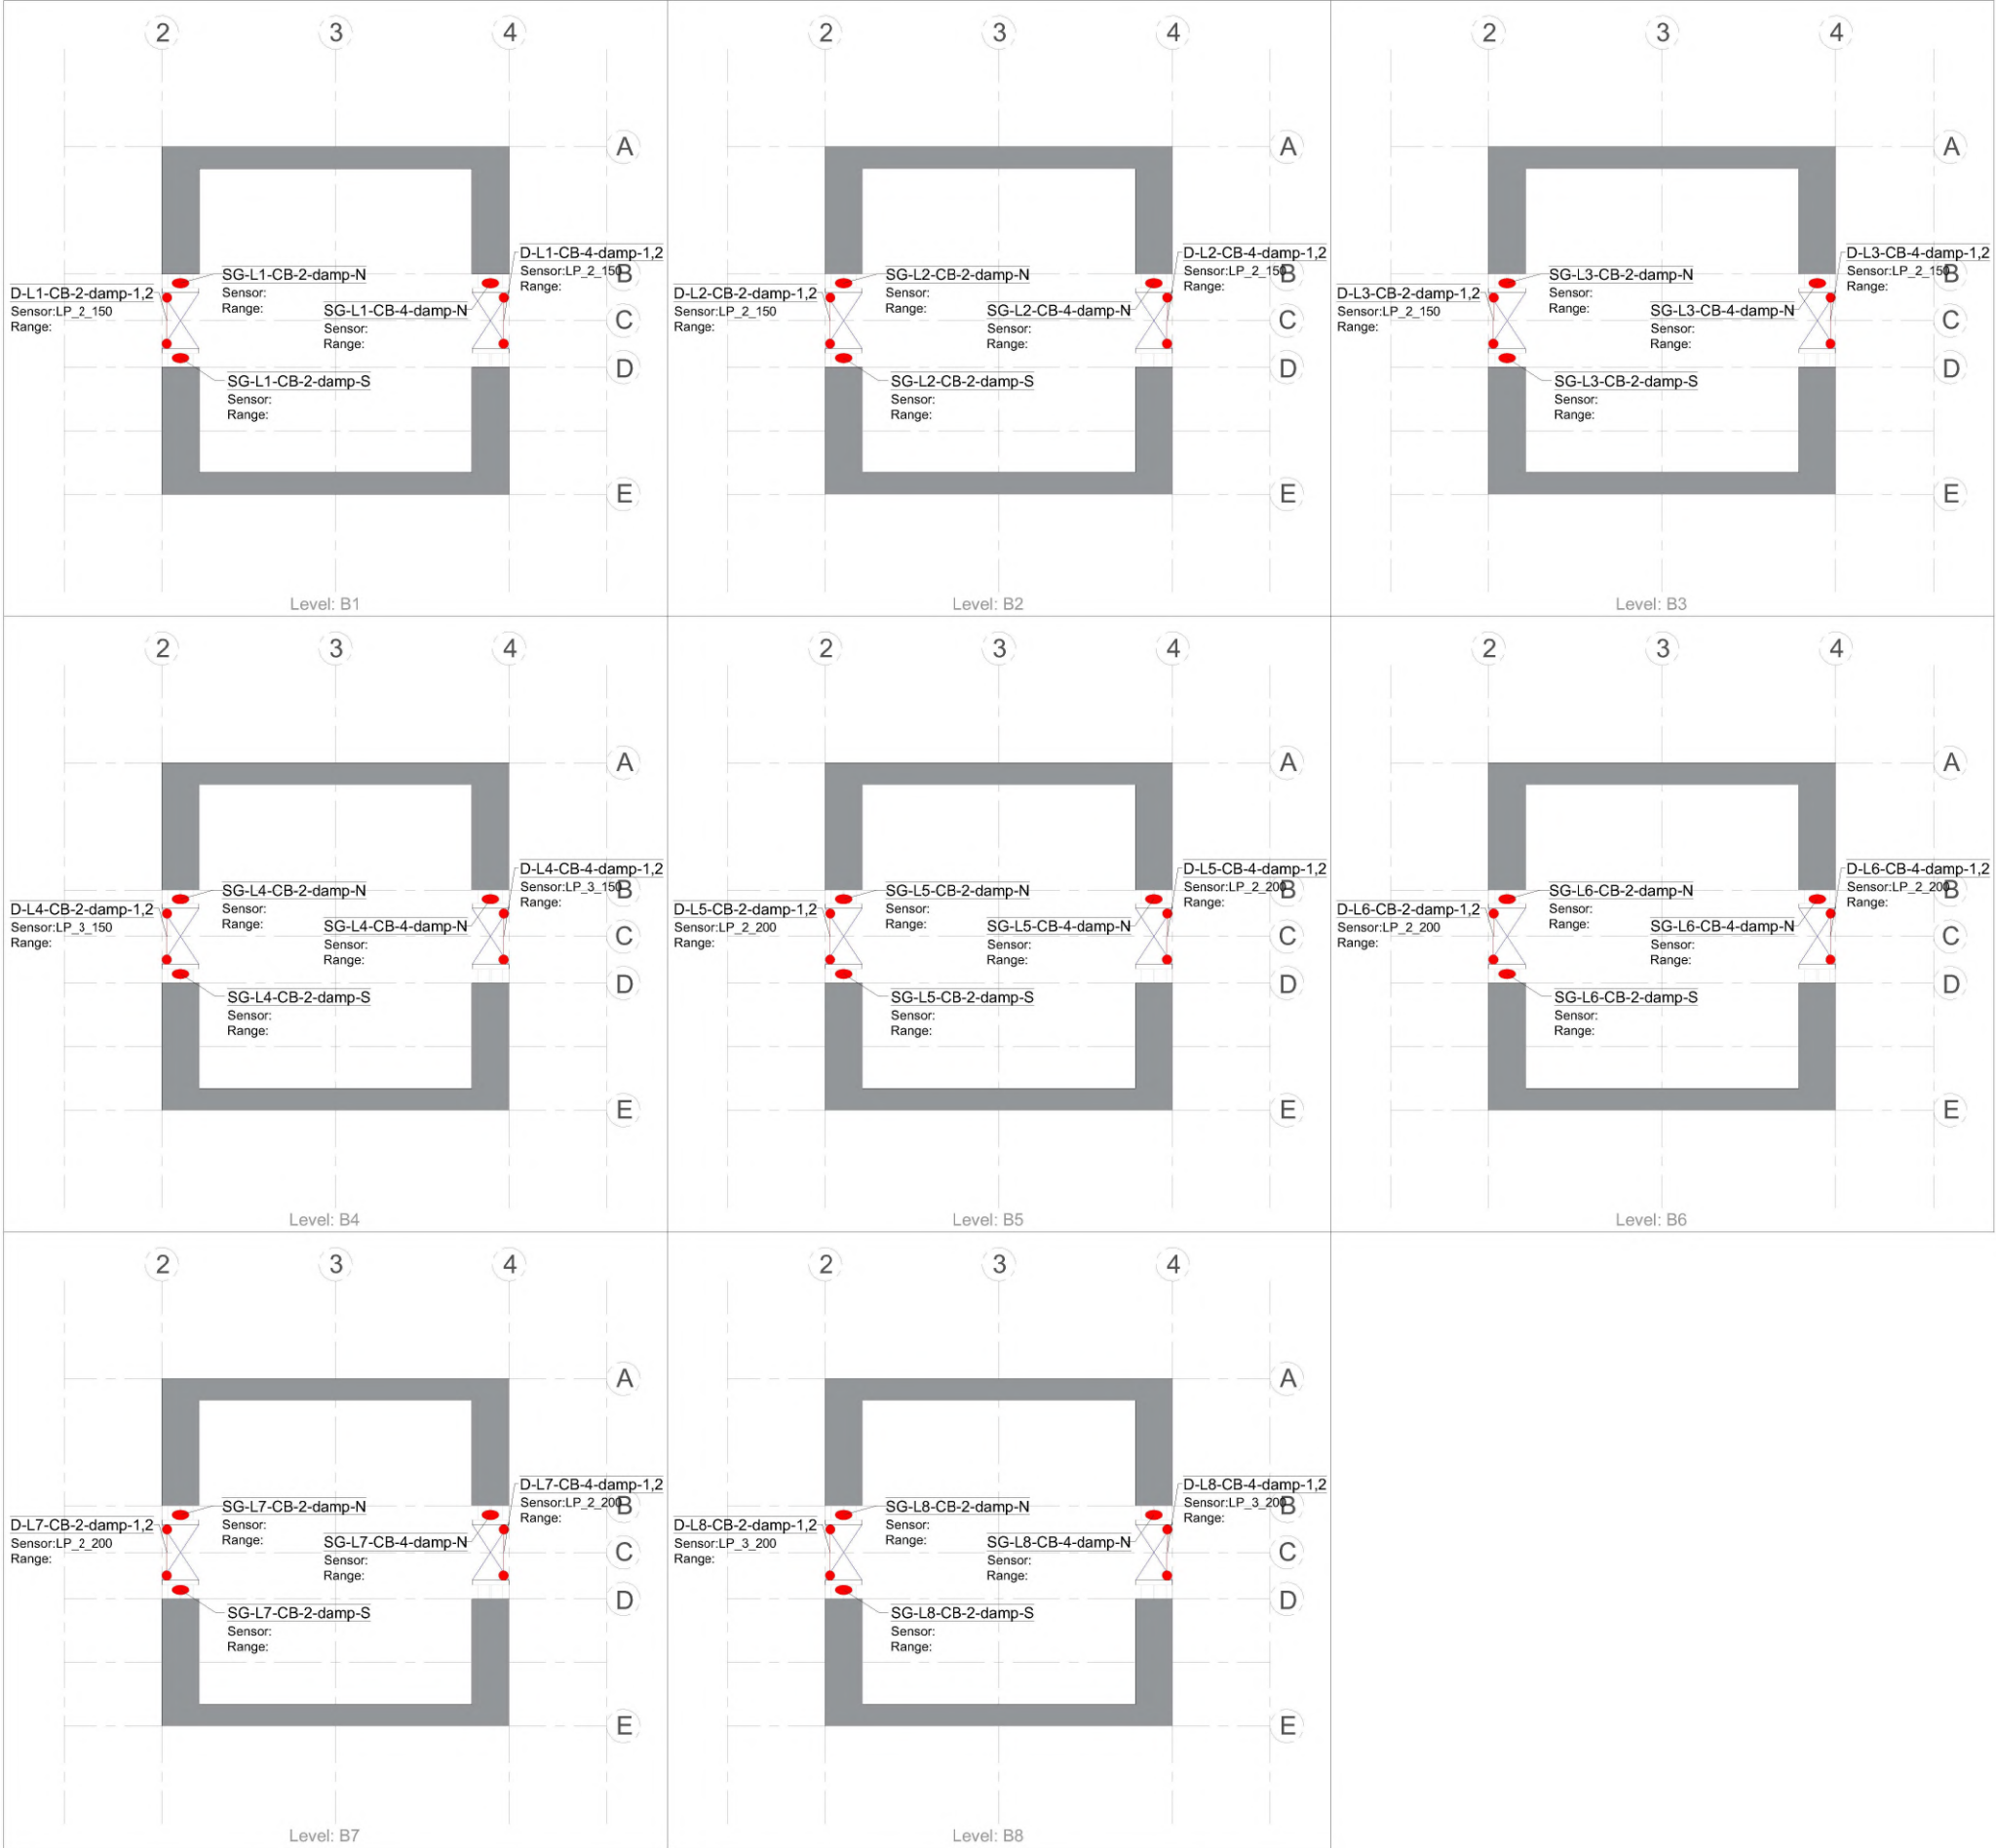


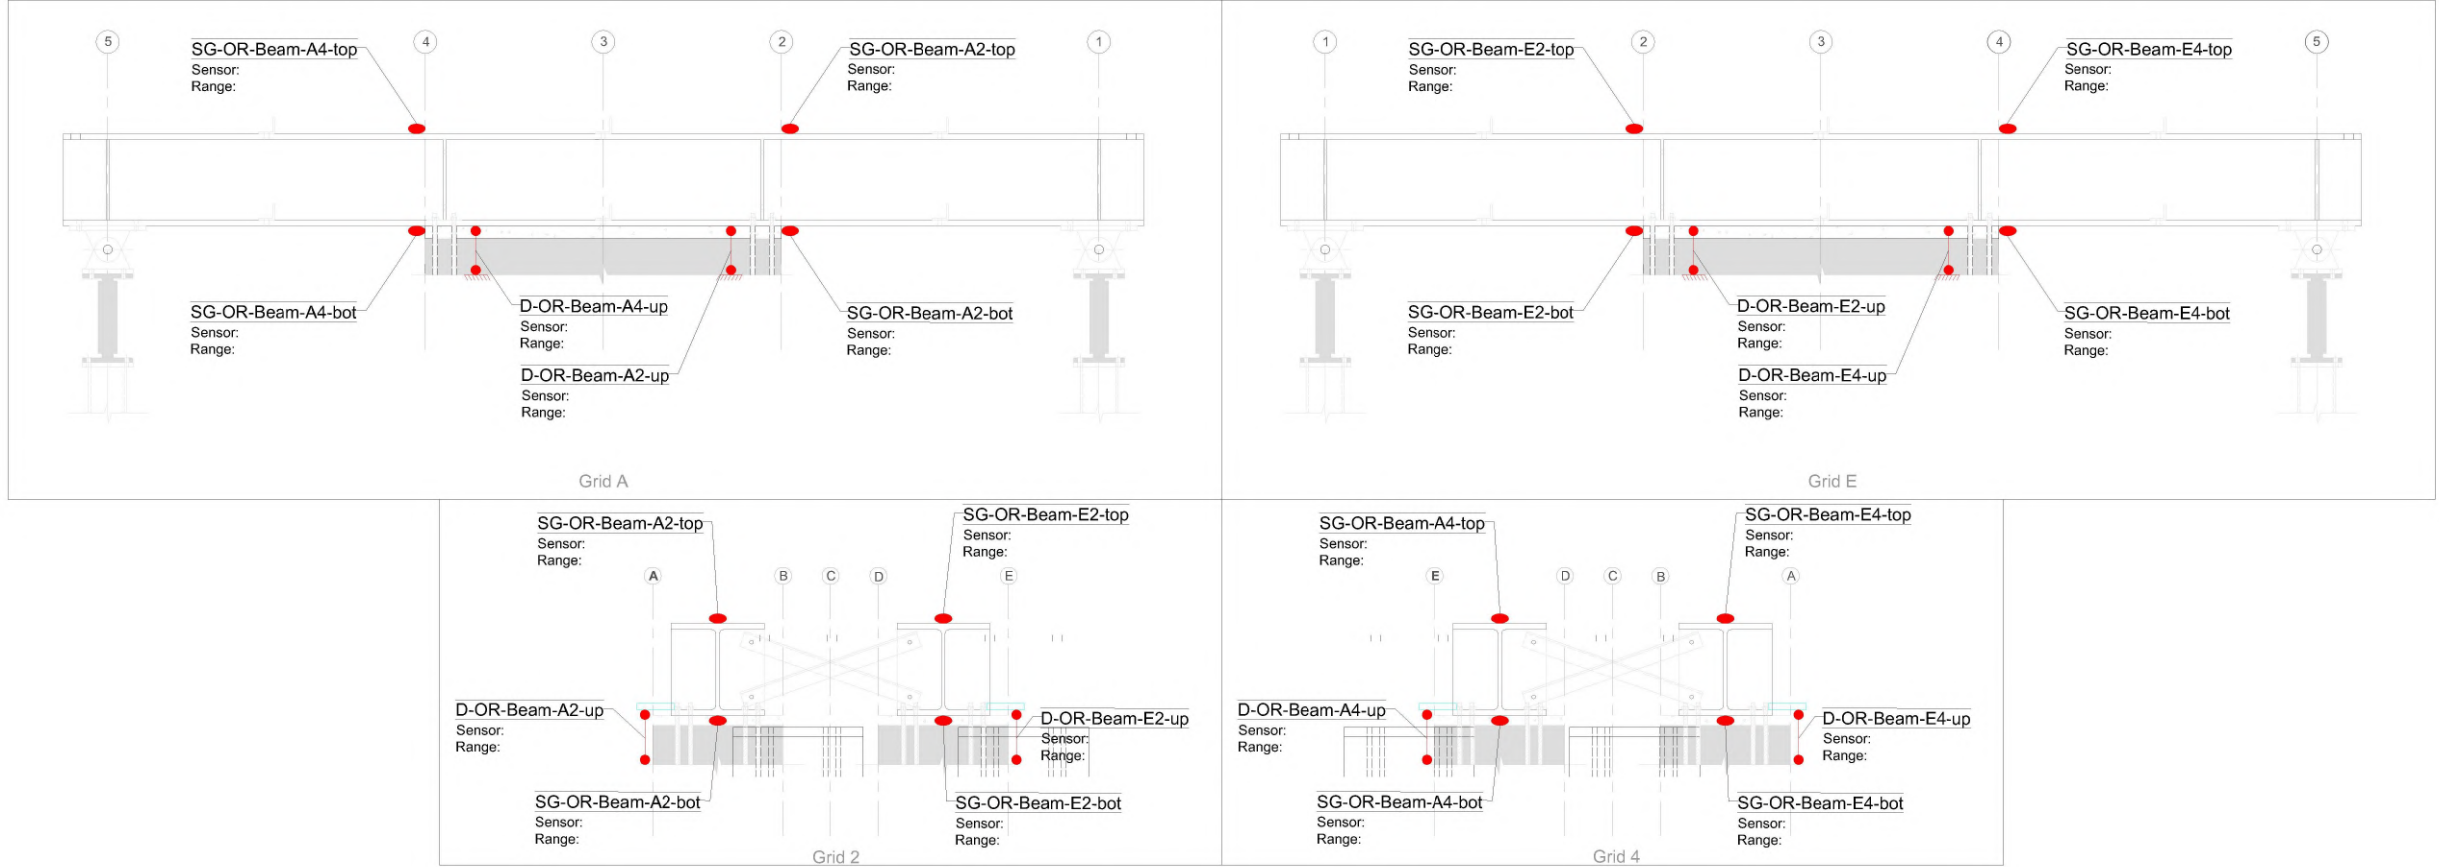


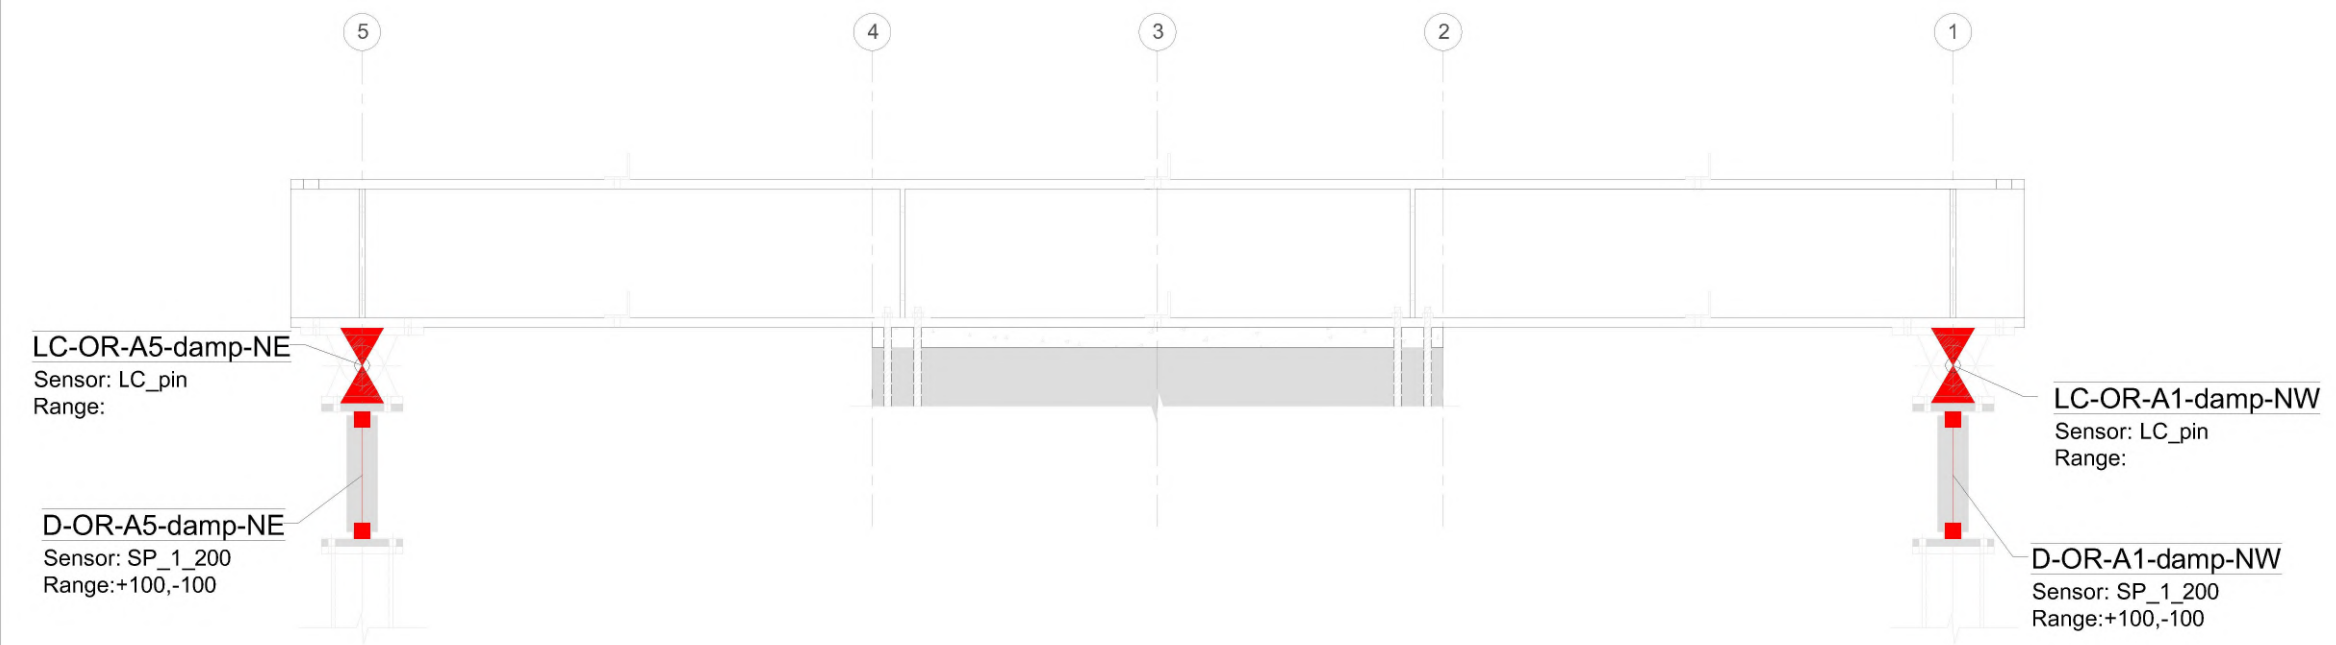


Grid A

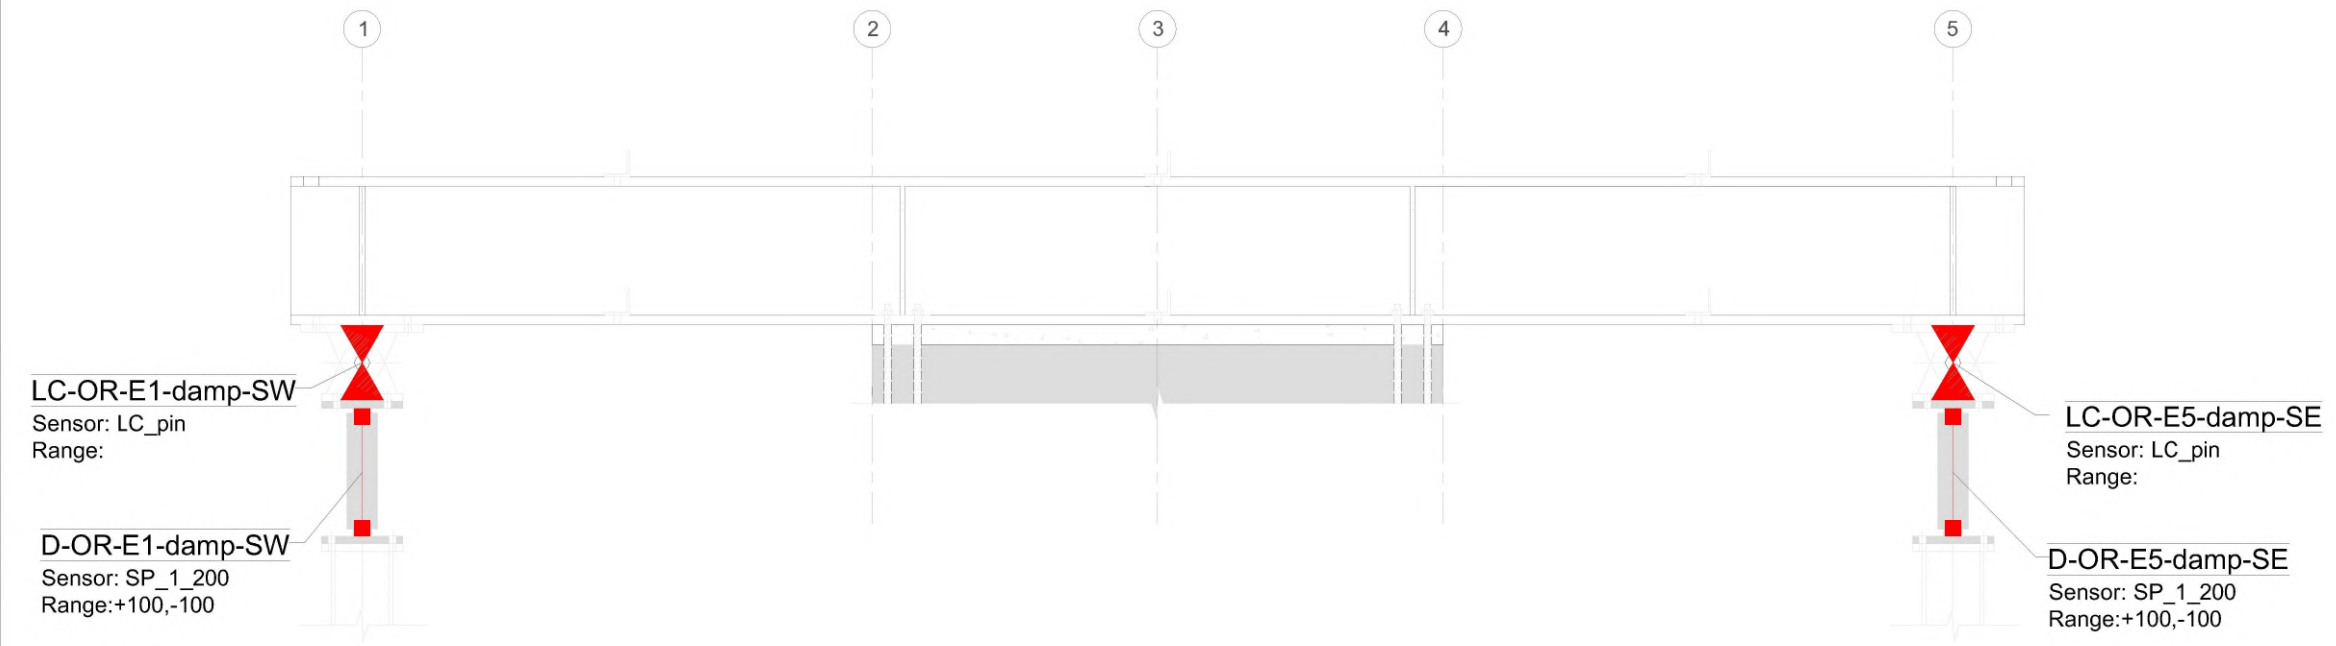


Grid E

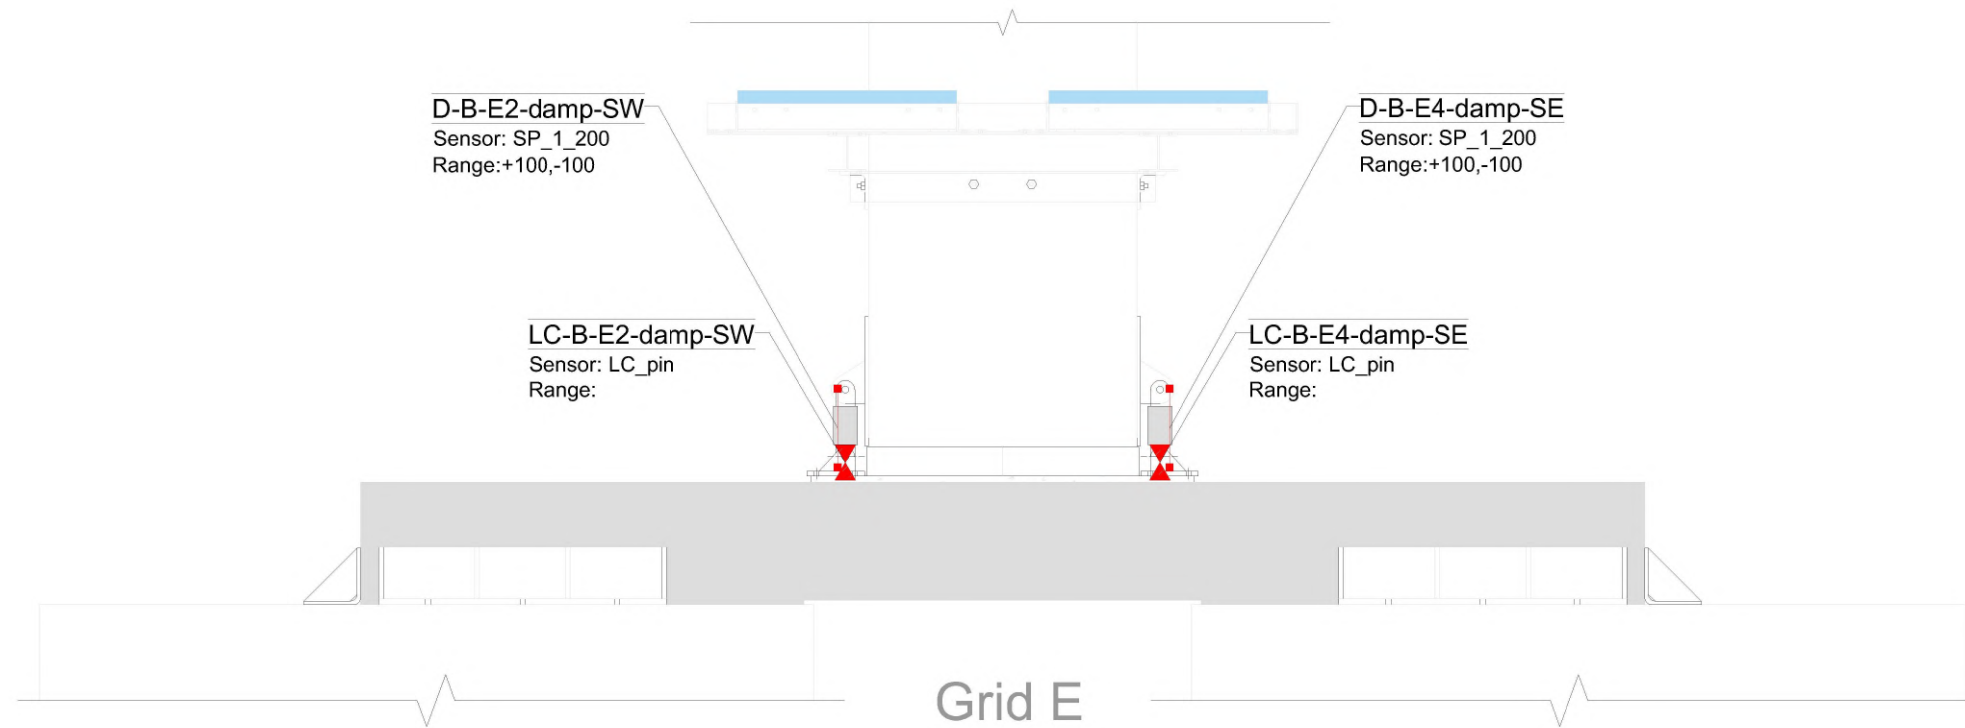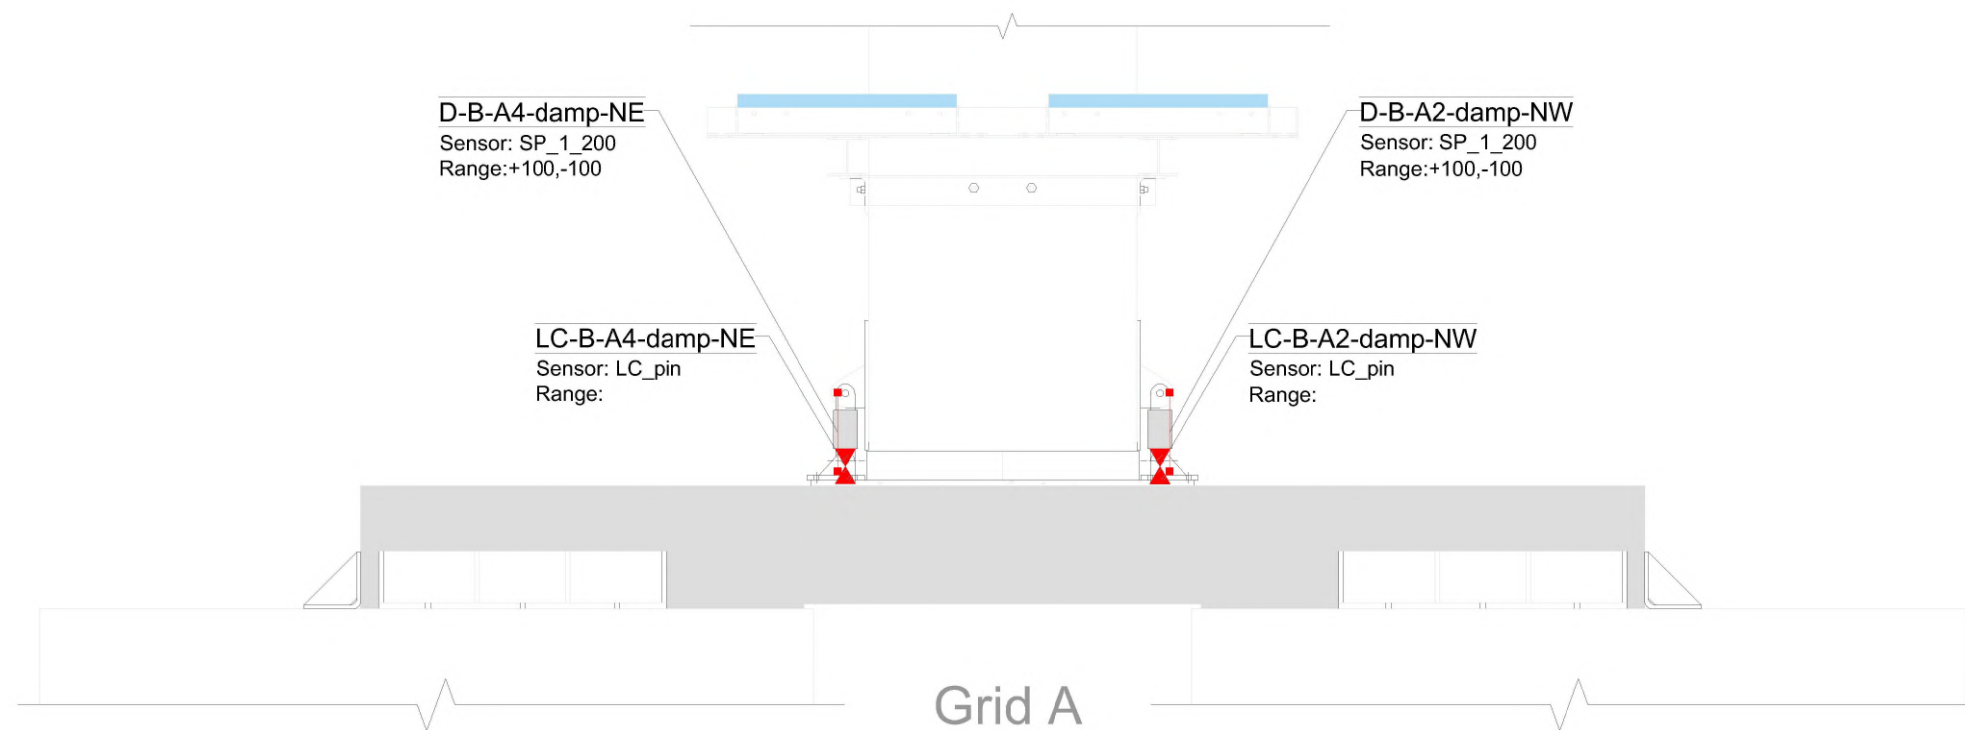

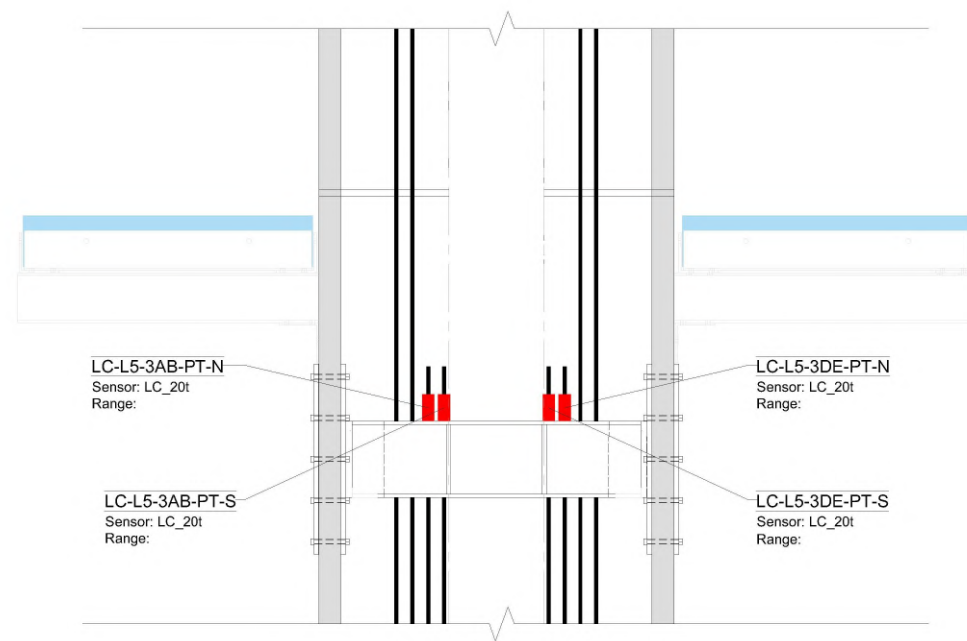

Grid 3

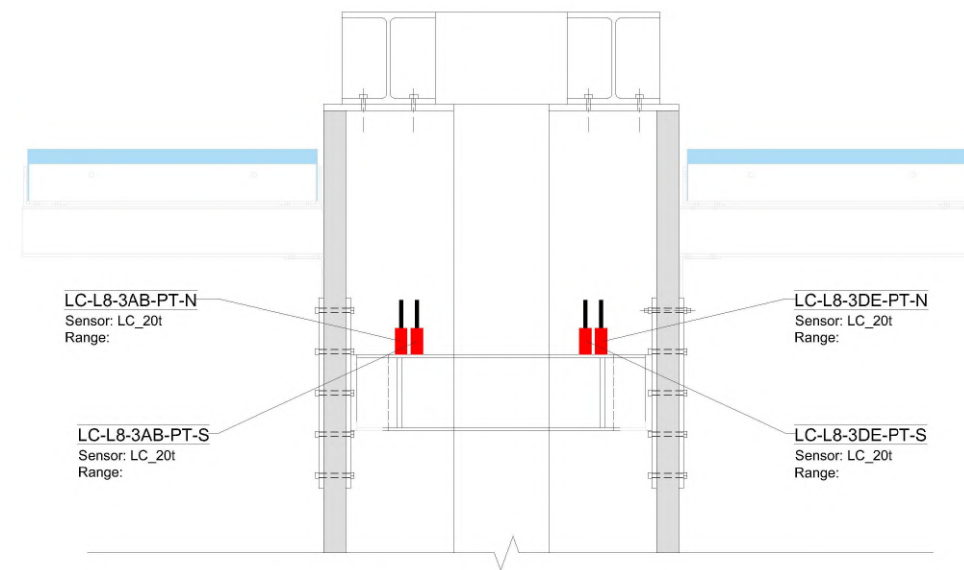

Grid 3



**Local Force
Base Dampers**

SHEET NO.

12

DRAWN BY

Amin Sadeghi
Henry Xu
Lisa Tobber

DATE Oct-2019

Scale 1:30